

## **ESPECIFICACIONES TÉCNICAS**



**Proyecto:**

***“HABILITACIÓN BODEGAS DE ALIMENTO: MUEBLERÍA  
A MEDIDA RESIDENCIA UNIVERSITARIA MARIO OJEDA  
Y AMANDA LABARCA 2026,  
UNIVERSIDAD DE CHILE”***

- **Marín 525, comuna de Providencia. Santiago.**
- **Riquelme 260, comuna de Santiago.**

**Dirección de Bienestar y Desarrollo Estudiantil**

**UNIVERSIDAD DE CHILE**

***25 DE JUNIO DE 2026***

**Elaborado por:** Eduardo Rojas Cortez

## **0. INFORMACIONES GENERALES**

### **0.1 MATERIA Y UBICACION DE LA OBRA**

Las presentes Especificaciones Técnicas corresponden a las necesarias para la ejecución de trabajos de mejoramiento de recintos en el inmueble Residencia Universitaria femenina Mario Ojeda, ubicada en la calle Marín 525, comuna de Providencia y Residencia Universitaria masculina, ubicada en Riquelme 260 comuna de Santiago. Ambos inmuebles a cargo de la Dirección de Bienestar y Desarrollo Estudiantil (DIRBDE).

### **0.2 PROPIETARIO**

Universidad de Chile.

### **0.3 PROFESIONALES**

DIRBDE – Unidad de Gestión y Proyectos

### **0.4 ANTECEDENTES PARA LA EJECUCION DE LA OBRA.**

#### **ARQUITECTURA**

- Planos de Arquitectura.
- Detalles de Arquitectura.
- Especificaciones Técnicas de Arquitectura.

### **0.5 GENERALIDADES**

#### **0.5.1 Disposiciones Generales.**

Las presentes Especificaciones Técnicas (EETT) son de carácter general y se refieren principalmente al enfoque del mejoramiento, habilitación y remodelación de recintos comunes de las dependencias de la Residencia Universitaria Mario Ojeda, de la Universidad de Chile. En todos los casos, las obras materiales y sistemas constructivos que se apliquen deberán estar dentro de las Normas y Reglamentos vigentes sobre la materia y se entienden conocidos por el Contratista y forman parte integrante de estas Especificaciones Técnicas. Este documento determina los materiales en cuanto a su procedencia, características, calidades y los métodos de construcción, requeridos para las obras correspondientes al proyecto mencionado. La responsabilidad en estas obras será del contratista.

Nota general, válida para todos los materiales de construcción: Los materiales especificados con marcas, salvo indicación expresa, son referenciales y podrán ser reemplazados por otros de características técnicas y estéticas equivalentes o superiores. Cualquier reemplazo deberá ser aprobado previamente por la IFO, y en todo caso sus características ignífugas no pueden ser inferiores. Dentro de cada partida se incluye el traslado de materiales, artefactos, herramientas hasta el inmueble, a pesar de que se omite textualmente en cada partida en las presentes Especificaciones técnicas. Se debe tener total conocimiento que en los casos que se deba realizar alguna obra complementaria como picar muro para tener acceso a algún tipo de cañería o algún otro tipo de daño a la estructura o apariencia existente de cualquier parte constituyente del inmueble, sin perjuicio que la reparación sea omitida en las presentes EETT, se deberán recepcionar las instalaciones tal cual fueron entregadas al contratista, sin cargo adicional para la Universidad. Se contemplan aquí las faenas imprescindibles para la óptima y total realización de la obra, aunque alguna partida no se mencione en estas Especificaciones Técnicas por error, omisión o porque se consideró obvia su inclusión.

### **0.5.2 Campo de Aplicación.**

Las presentes EETT son de aplicación obligatoria en todas sus partes, salvo disposiciones taxativas en contrario consignadas en los planos o en documentos expresamente modificatorios.

### **0.5.3 Documentos que integran las Especificaciones Técnicas.**

En todo aquello que sea aplicable a las obras materia del proyecto y salvo disposiciones taxativas en contrario, se tendrán como parte integrante y/o complementaria de las presentes especificaciones técnicas los siguientes documentos:

#### **0.5.3.1 Leyes Ordenanzas y Reglamentos.**

- Ordenanza General de Urbanismo y Construcciones. Edición Vigente.
- Ley General de Urbanismo y Construcción.
- Ordenanza Local de Providencia.
- Reglamento de construcción y Proyectos de Redes de Distribución de Energía Eléctrica en alta y baja tensión.
- Reglamento de Instalaciones de Alumbrado y Fuerza Motriz Interiores.
- Reglamento de la S.E.C. (Electricidad y Gas).
- Reglamento de Instalaciones de Alcantarillado y Agua Potable (RIDAA)
- DS N° 50 MINVU Modificación al DS N° 458/ 15 06 2016.
- Código del Trabajo en especial art 157. En los casos en que las infracciones por parte de los trabajadores a las normas de los reglamentos internos se sancionen con multa, ésta no podrá exceder de la cuarta parte de la remuneración diaria del infractor.
- Normas chilenas del INN, definirán materiales de construcción, medidas de seguridad y todo aspecto aplicable en cada una de las áreas sujetas a las referencias de la OGUC o en ausencia de otras normas.
- Ley 20.703/ MINVU; Crea y regula los registros nacionales de inspectores técnicos de obra (ITO) y de revisores de proyectos de cálculo estructural, modifica normas legales para garantizar la calidad de construcciones y agilizar las solicitudes ante las direcciones de obras municipales.
- D N° 85 DO 30 10 2007 MINVU. Promulgado el 13 04 2007 Manual de Inspección Técnica de Obras.
- Ley 20.422/2010 (normas sobre la igualdad y la inclusión social).
- Ley 21.015/ 2016 (Incentiva la Inclusión de Personas con Discapacidad al Mundo Laboral).
- DS N° 594 MINSAL Condiciones Sanitarias en los lugares de Trabajo.
- NCH 1433 OF. 78 Ubicación y señalización de Extintores.
- DN° 50 MOP (28.01.2003) Aprueba el reglamento de instalaciones domiciliarias de agua potable y de alcantarillado.

#### **0.5.3.2 Bases o Pliegos Administrativos.**

Contratos y sub-contratos que regulen las relaciones entre el Propietario y la EC, o entre la EC y sus proveedores. Estos documentos se emitirán cuidando de no incurrir en contradicción con las disposiciones de las presentes EETT o con las indicaciones en los planos.

#### **0.5.3.3 Planos.**

La determinación gráfica de las obras se encuentra expresada en los planos emitidos por los Arquitectos y especialistas del ámbito eléctrico.

#### **0.5.3.4 Normas Chilenas.**

- Normas relacionadas con medidas de seguridad.
- Normas relacionadas con calidad y Métodos de ensayos.
- NCH 1433 OF. 78. Ubicación y señalización de Extintores.
- Y toda norma chilena vigente a la fecha.

#### **Margen de aplicación de las Normas Chilenas.**

Todo elemento, material de construcción o procedimiento empleado en la construcción, deberá cumplir y/o ejecutarse en estricto acuerdo con las normas vigentes a la fecha.

Las normas relacionadas con el personal y medidas de seguridad son de aplicación obligatoria en todas sus partes.

Las normas relacionadas con calidad y métodos de ensayos son de aplicación obligatoria en todo aquello que no se oponga a disposiciones taxativas de las presentes especificaciones o a indicaciones gráficas o textuales consignadas en los planos.

#### **0.5.4 Personal.**

El personal técnico superior a cargo de la obra deberá estar compuesto como mínimo por un Técnico en Construcción o superior. La Empresa Constructora (EC) desplegará en la obra, los obreros, necesarios para asegurar el correcto funcionamiento de los diferentes servicios internos, como también lo referente a la seguridad industrial del personal mismo. Por tratarse de obras en un edificio ocupado por funcionarios y estudiantes de la Universidad, la EC dotará y exigirá a todos los obreros, elementos de máxima seguridad para el buen desarrollo y eficiencia de sus funciones. La IFO exigirá, tanto a la EC como a los Subcontratos (SSCC), que doten a sus trabajadores de las máximas medidas de seguridad que el sentido común y la Ley Laboral exige, aparte de los seguros y cumplimiento de las Leyes que protegen a los trabajadores. En cumplimiento de lo anterior, no se debe permitir obreros que trabajen sin implementos (zapatos de seguridad, cinturón de seguridad, casco, guantes, etc.). El operario que no respete esta disposición debe ser sancionado. La EC debe llevar control de implementos entregados a los obreros para cumplir la disposición y exigirla. Por tratarse de obras que se realizarán en lugares cercanos a equipos o personas de la Universidad, la EC deberá extremar las medidas de seguridad que eviten interferencias, accidentes y daños a la propiedad. Para estos efectos la EC deberá presentar las medidas de seguridad que implementará, suscritas por el profesional del área de prevención de riesgos y suscribir las pólizas de seguro que el Mandante le indique.

#### **0.5.5 Archivo de la Obra.**

Bajo la responsabilidad del Profesional residente de la Obra y bajo su custodia, se mantendrá en la oficina de la faena (recinto destinado dentro del inmueble por parte de administración) un archivo de los siguientes documentos debidamente encuadernados y ordenados:

- Leyes, Ordenanzas y Reglamentos. Bases o Pliegos Administrativos.
- Colección completa de Planos expuestos en panel y debidamente protegidos.
- Las presentes EETT, incluidas sus eventuales Fe de Erratas y las consultas sobre aclaraciones y sus respectivas resoluciones en un Libro Técnico o en el libro de obra.

#### **0.5.5.1 Planos, Especificaciones Técnicas u otros documentos.**

Sin perjuicio de la facultad de la EC para solicitar, a su costa, la cantidad de copias de planos o especificaciones que se requieran del archivo de la oficina de los Arquitectos, deberá disponerse en la oficina de la faena - bajo custodia y responsabilidad de la IFO - de un ejemplar debidamente encuadernado de las Bases Administrativas, EETT, Contratos, presupuestos y demás documentos de texto, así como un juego completo de los planos que se mantendrán desde la iniciación hasta el término de las faenas y no se podrán reemplazar por otros similares, salvo expresa autorización escrita y firmada por todos los interesados. Esta disposición tiene por objeto conservar debidamente las anotaciones que la IFO desee efectuar, ya sea a título aclaratorio o modificadorio, en cualquier etapa del desarrollo de las obras. Estos planos serán firmados por el Jefe de Obras y por el representante de la IFO.

#### **0.5.5.2 Libro de Obra.**

No aplica.

#### **0.5.5.3 Guías de Materiales.**

La EC mantendrá un control de materiales de Bodega en donde se registren las entradas y salidas de materiales, hacia y desde el recinto de las faenas, como asimismo todos los ingresos de materiales a la obra.

#### **0.5.5.4 Certificados de Ensaye de Materiales.**

No se consulta certificados de ensaye de materiales

#### **0.5.6 Sub-contratistas de la E.C.**

Los Subcontratos de especialidades de obras, deberán contar con la aprobación de la IFO y su designación será sometida a la calificación del Propietario, el cual queda facultado para aprobar o rechazar la proposición de la EC.

#### **0.5.7 Permisos, Aprobaciones e Inspecciones.**

No se consulta la tramitación de permisos.

#### **0.5.8 Interpretación de Planos.**

##### **0.5.8.1 Aclaraciones durante el período de estudio de la propuesta.**

La EC deberá informar por escrito cualquier duda que le merezca la interpretación de los planos, la descripción de las EETT y/o de sus documentos anexos. Se entenderá que la EC asume, sin reservas de ninguna especie, las indicaciones de los diseños y las descripciones contenidas en los citados documentos y que no fuesen objeto de reparos o consultas. Las consultas serán aclaradas por intermedio del mandante, en un plazo establecido según Bases Administrativas.

##### **0.5.8.2 Aclaraciones ulteriores al estudio de la propuesta.**

No obstante, lo anterior, cualquiera duda que se presente a la EC durante la ejecución de las obras, deberá someterla a la resolución de la IFO en quien exclusivamente, reside la facultad para dictaminar con relación a interpretación de planos y especificaciones. La EC deberá acatar el dictamen de la IFO sin que pueda pretender aumento de plazo o precio, ni indemnización alguna con motivo de dicho dictamen, considerándose que la duda extemporánea es de absoluta responsabilidad de la EC. Como norma general, salvo evidente error, omisión o discordancia con lo establecido en general en el proyecto, en los casos de eventual contradicción primarán las indicaciones en los planos sobre los textuales.

## **1. GASTOS ADICIONALES, OBRAS PROVISIONALES Y TRABAJOS PREVIOS**

### **1.1 OBRAS PROVISIONALES**

#### **1.1.1 Instalaciones provisionales**

Será de costo y cargo del Contratista la implementación de las instalaciones provisionales que se utilicen durante el desarrollo de los trabajos, ya sean cierros temporales, andamios, letreros de advertencia, entre otros. Asimismo, se podrán utilizar los empalmes de electricidad y agua para el desarrollo de los trabajos, siendo los consumos de cargo de la Universidad, teniendo especial cuidado con la sobrecarga eléctrica por las herramientas a utilizar, si fuese necesario considerar diferencial para conexión de obra. Para estos efectos se podrán considerar las instalaciones existentes, asegurándose que no produzcan alteración en la prestación para otros recintos ocupados por la Universidad.

La utilización de la infraestructura existente deberá ser ejecutada de acuerdo con la normativa vigente sobre la materia y coordinada y aprobada por la IFO. Los eventuales daños que se puedan producir en instalaciones y equipos de la Universidad serán de costo y cargo del Contratista.

Dentro de este ítem se consideran andamios metálicos con ruedas y freno para todo tipo de trabajo en altura, de dos o más cuerpos de acuerdo con requerimientos, con crucetas y tablón metálico con fijaciones; equipos de seguridad, cierros, etc.

#### **1.1.2 Instalaciones de faenas**

Se designará recinto para bodega, oficina técnica, comedor y baño de servicio para trabajadores dentro del inmueble en cuestión. Los daños que pudiesen efectuarse en estos espacios, debido al uso por parte de la EC, deberán ser resueltos sin costo adicional para la Universidad.

#### **1.1.3 Aseo y cuidado de la obra**

Deberá extremarse la mantención periódica del aseo durante el desarrollo de los trabajos, en las áreas intervenidas, como también en vías de acceso, tránsito, etc.

Al término de las obras, como faena previa a la recepción provisoria sin observaciones, se efectuará el aseo total y cuidadoso del área intervenida, prestando especial atención a la limpieza de vidrios, artefactos sanitarios, elementos de cerrajería, pisos, cielos, muros, alfombras, etc. Esta faena deberá realizarla personal especializado en el rubro del aseo, con maquinarias, accesorios y productos de limpieza acorde a la superficie a limpiar

#### **1.1.4 Extracción de escombros**

El retiro será ordenado y en horarios que no interfiera con el movimiento de personal de las instalaciones. El contratista deberá proveer los insumos necesarios para efectuar oportunamente dicha labor. Los desechos y escombros deberán ser llevado a botadero autorizado (Certificado que deberá entregar al término de las faenas donde acredite el lugar de disposición final de los residuos o escombros). Para acumulación de material diario se facilitará espacio delimitado en patio trasero.

## **2. MUEBLERÍA**

### **2.1 Estantería metálica acero inoxidable 5 pisos estándar**

Se consulta la fabricación e instalación de estantería metálica estándar en Bodega de Alimentos compartida, con 5 pisos regulables, de acero inoxidable plegado 2mm. Las medidas aproximadas deben ser de 0,5 ancho x 1,0 m largo x 2 m alto. La estructura deberá ser resistente al ser cargada, sin deformaciones en bandejas ni verticales. Cada bandeja deberá tener una capacidad de carga no inferior a 80 kg, con nervadura central para evitar deformaciones. La estructura deberá estar reforzada con escuadras en sus esquinas y la bandeja inferior, deberá estar sobre una altura de 6 cm desde el nivel del piso. La instalación de la estantería deberá ser mediante pernos, tuercas y golillas, en donde cada pata deberá poder fijarse con la adyacente mediante el sistema mecano. No se deben fijar a piso, ya que deben quedar con opción de moverse.


### **2.2 Estantería metálica acero inoxidable 5 pisos a medida**

Se consulta la fabricación e instalación de estantería metálica a medida, con 5 pisos regulables, de metal acero inoxidable plegado 2mm. Las medidas aproximadas deben ser obtenidas a partir de planos y de corroboración en terreno. La estructura deberá ser resistente al ser cargada, con nervadura central en cada bandeja, sin deformaciones en bandejas ni verticales. Cada bandeja deberá tener una capacidad de carga no inferior a 80 kg. La estructura deberá estar reforzada con escuadras en sus esquinas y la bandeja inferior, deberá estar sobre una altura de 6 cm desde el nivel del piso. La instalación de la estantería deberá ser mediante pernos de anclaje, en donde cada pata deberá tener pletina perforada para fijar hacia el piso. Si se requieren fijaciones en muros, deberá considerarse dentro de esta partida.


### **2.3 Carro distribuidor**

Se consulta la provisión de carro distribuidor de alimentos, el cual deberá tener ruedas con capacidad para cargar un máximo de 150 kg. Las dimensiones deberán ser de 1,0 de largo x 0,5m de ancho. Deberá tener la cualidad de ser plegables, resistente y con superficie antideslizante. Materialidad aluminio. Marca Jamer o equivalente técnico.


INSTALACIÓN MUEBLERÍA BODEGA DE ALIMENTOS  
COMPARTIDA (RESIDENCIA MARIO OJEDA)  
esc. 1:25

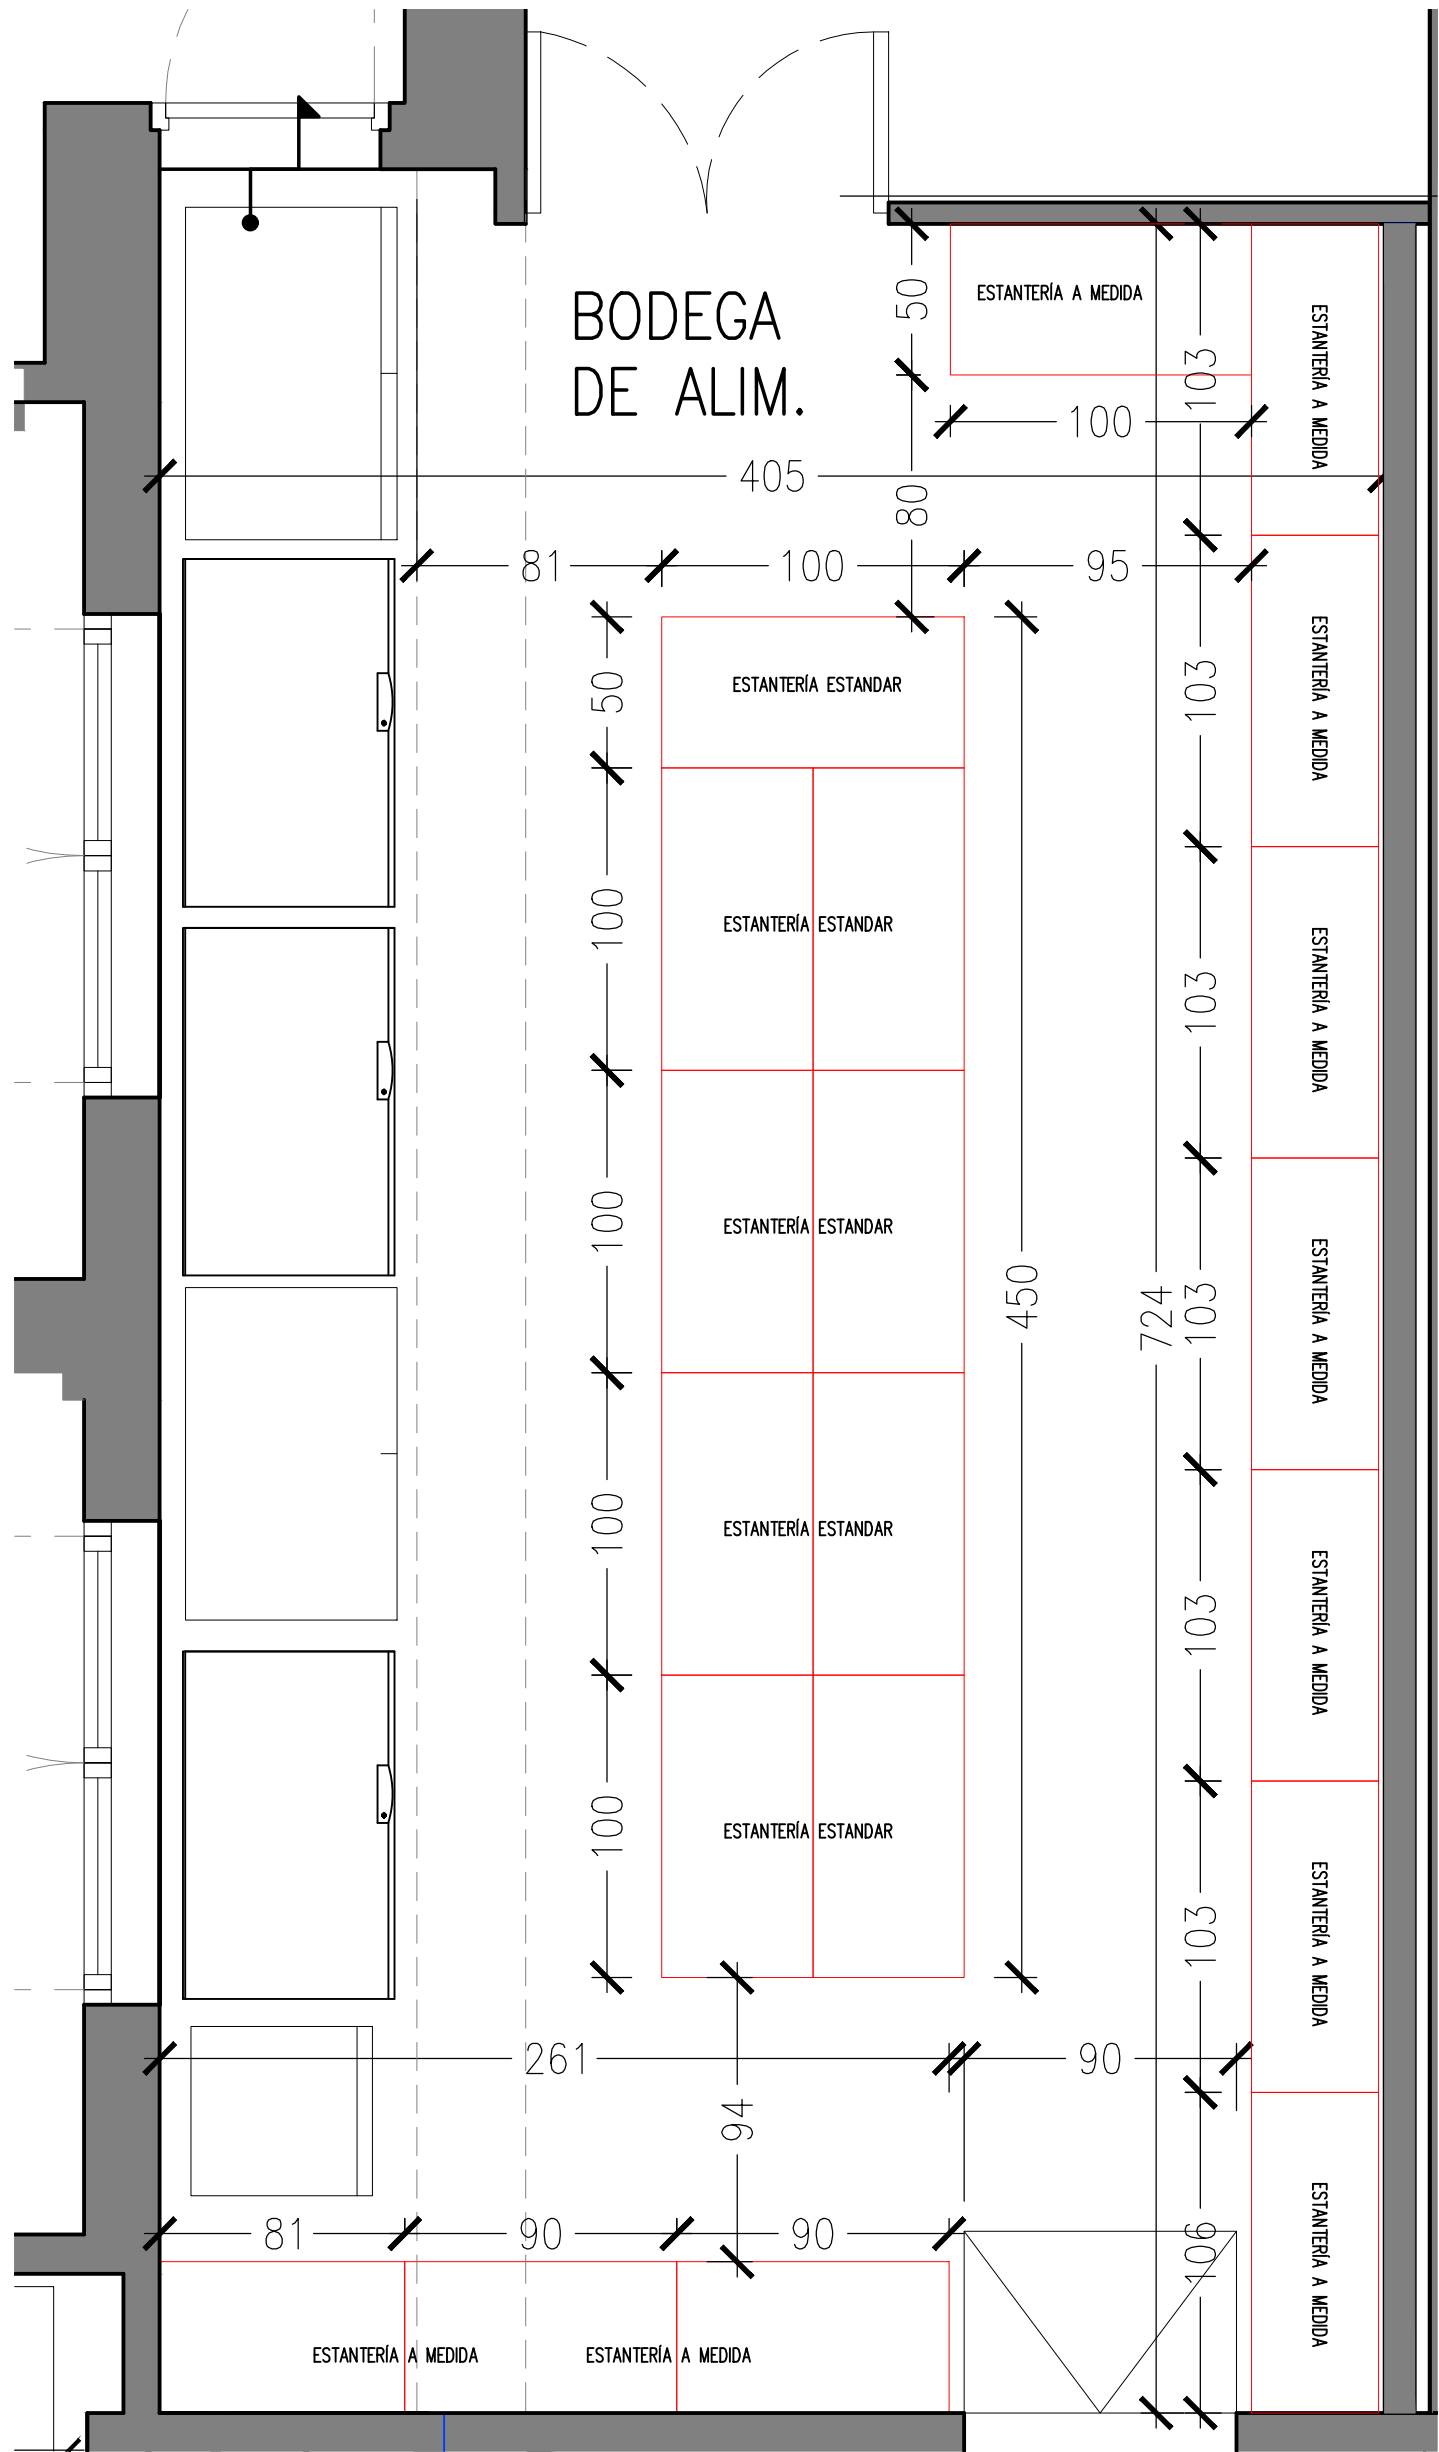


INSTALACIÓN MUEBLERÍA BODEGA DE ALIMENTOS  
RESIDENCIA MARIO OJEDA  
esc. 1:25

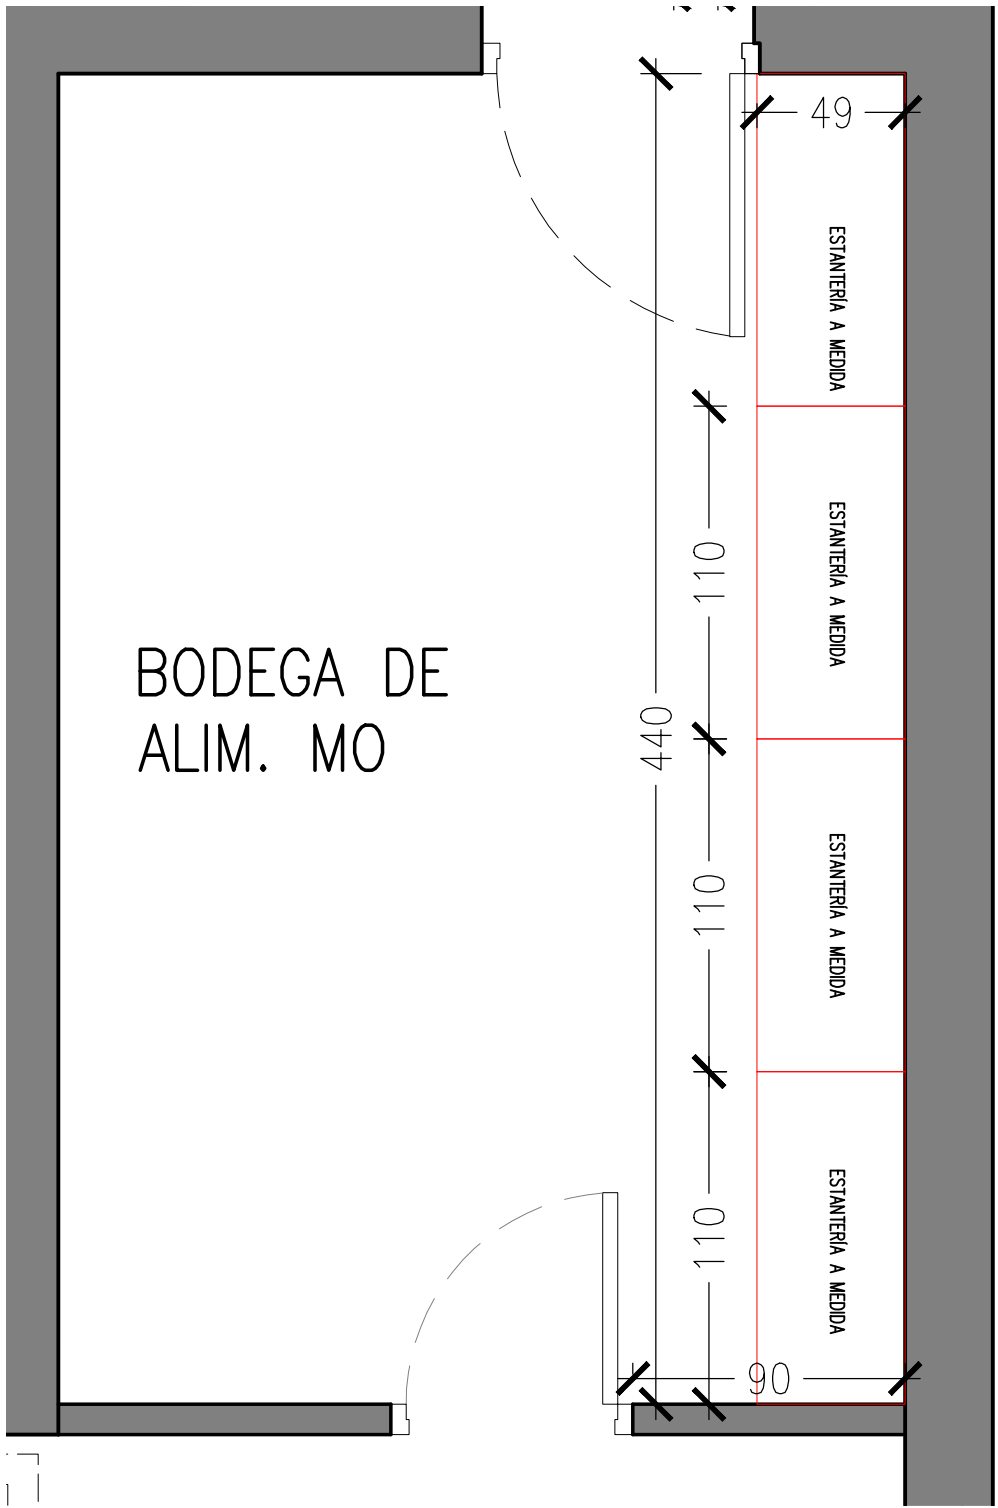


DETALLE ESTANTERÍA METÁLICA  
ACERO INOXIDABLE  
esc. 1:20

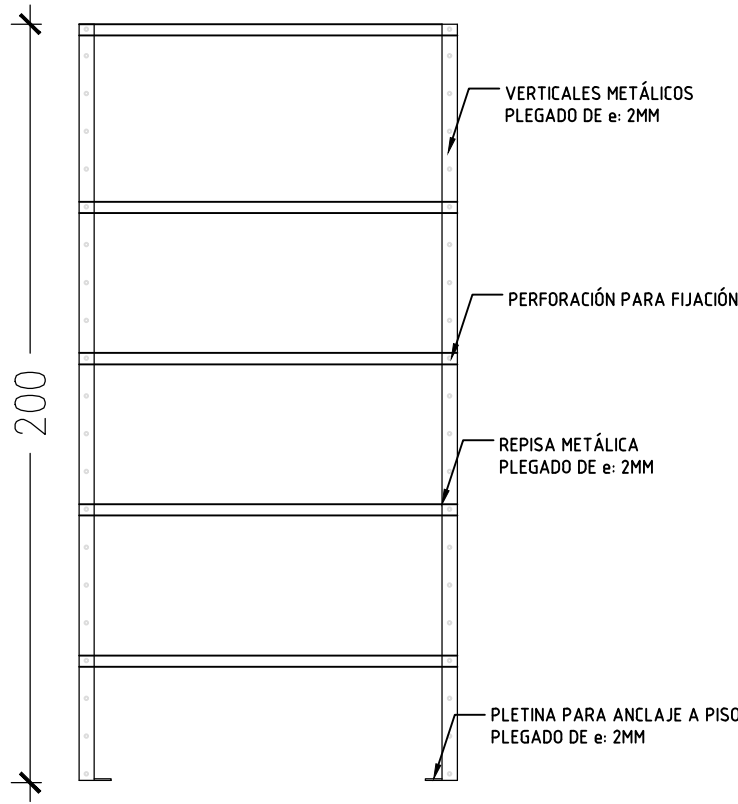


INSTALACIÓN MUEBLERÍA BODEGA  
RESIDENCIA AMANDA LABARCA  
esc. 1:25

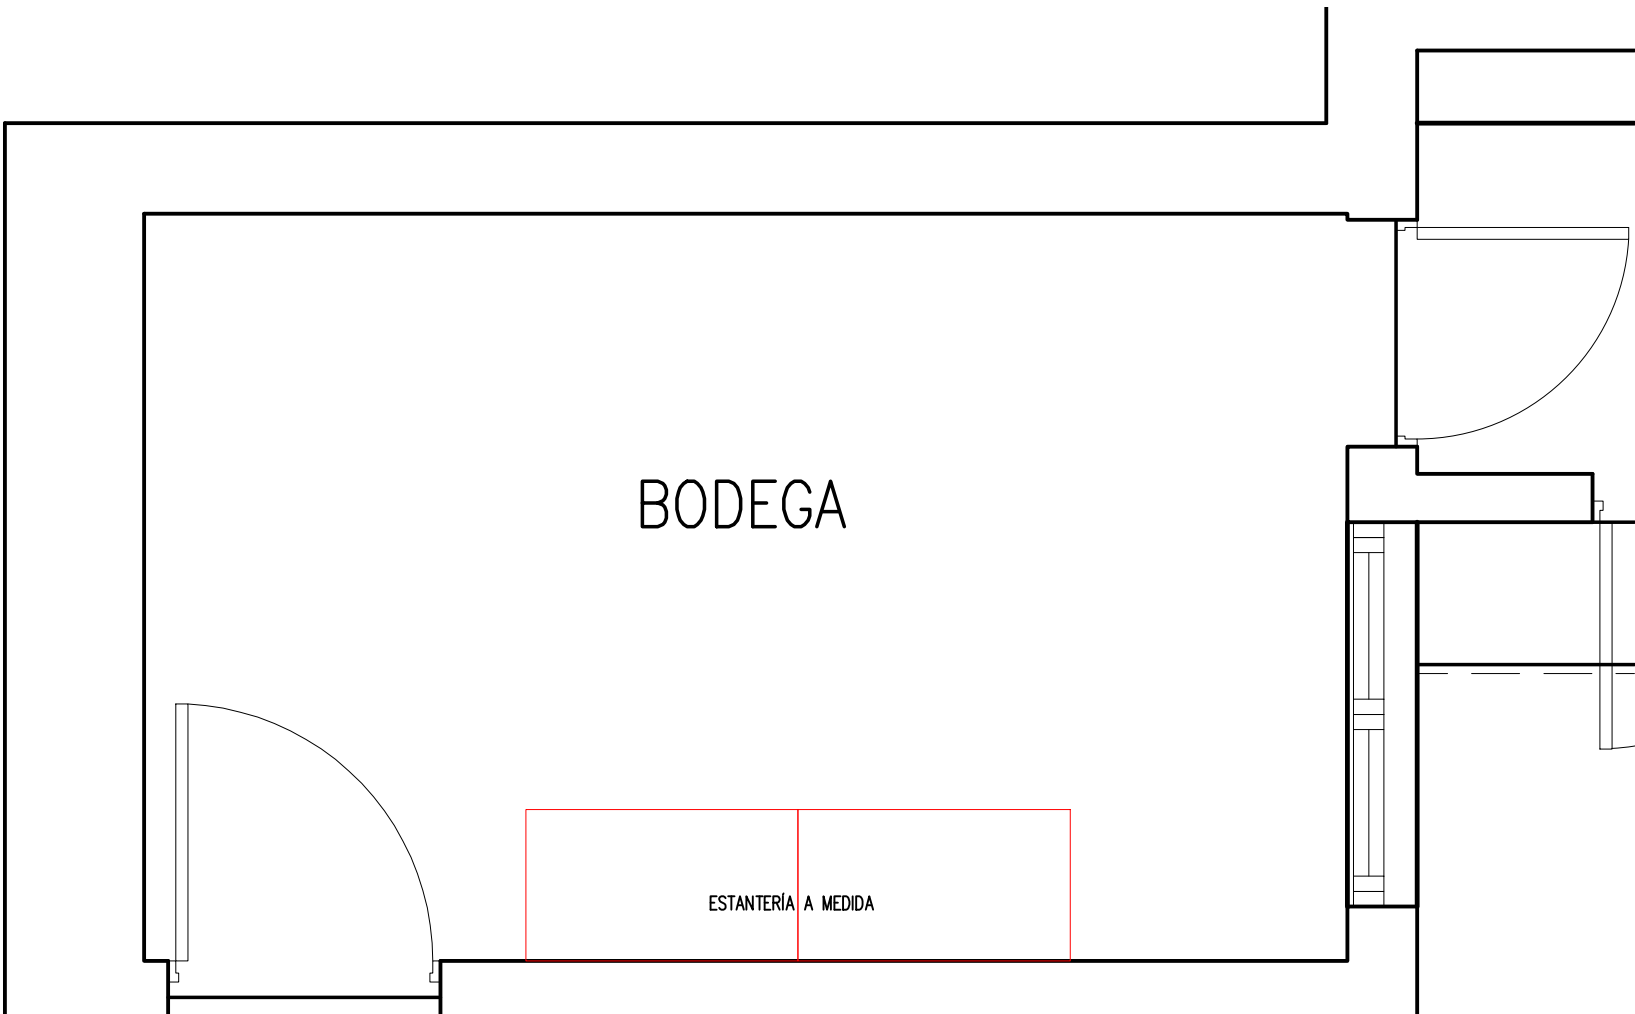

CARRO DE TRASLADO DE MERCADERÍA

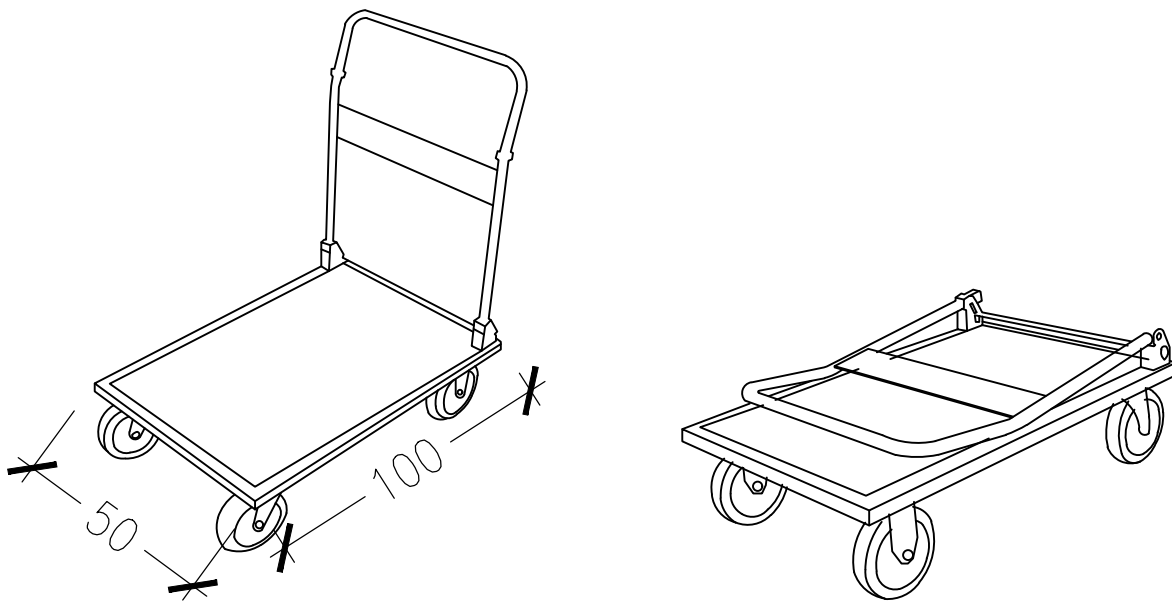

- NOTA
- \* ESTANTERÍA A MEDIDA SE REFIERE A AQUELLAS QUE DEPENDIENDO DE ESPACIO DISPONIBLE EN OBRA TERMINADA, SE DEBERÁ INSTALAR DE MANERA FIJA EN SECTOR SEÑALADO, SIEMPRE CONSIDERANDO APOYOS Y NERVADURAS.
  - \* ESTANTERÍA ESTÁNDAR, SE REFIERE A ESTANTERÍAS DE MISMAS DIMENSIONES SEÑALADAS EN PLANOS, LAS CUALES DEBERÁN QUEDAR FIJAS ENTRE SÍ, MEDIANTE TUERCAS Y TORNILLOS, ES DECIR, TIPO MECANO. ÉSTAS NO DEBERÁN SER APERNADAS A PISO, YA QUE DEBEN OFRECER LA POSIBILIDAD DE MOVILIDAD.
  - \* LAS PROFUNDIDADES DE LAS ESTANTERÍA, SE DEBERÁ CORROBORAR EN TERRENO. EL LARGO NO PODRÁ SUPERAR LOS 1,1 M ENTRE APOYOS.
  - \* SE CONSIDERA SOLO UN CARRO DISTRIBUIDOR.
  - \* EL SERVICIO DEBE REALIZARSE EN DOS DIFERENTES DIRECCIONES.
  - \* EL CARRO DISTRIBUIDOR DEBE SOPORTAR 150 KG, DEBE SER PLEGABLE Y CON SUPERFICIE ANTIDESLIZANTE EN SU SUPERFICIE.
  - \* TODAS LAS MEDIDAS DEBERÁN SER CORROBORADAS EN TERRENO UNA VEZ LOS TRABAJOS PREVIOS DE REMODELACIÓN, FINALCEN.
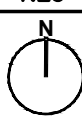
|   |  |                  |                                                                                       |
|---|--|------------------|---------------------------------------------------------------------------------------|
|  <div>UNIVERSIDAD DE CHILE</div> <div>Dirección de Bienestar y Desarrollo Estudiantil DIREDE</div> |  |                  |                                                                                       |
| PROYECTO   |  |                  |                                                                                       |
| MEJORAMIENTO DE RECINTOS R.U.   |  |                  |                                                                                       |
| DIRECCION   |  |                  |                                                                                       |
| MARIN N°0525 PROVIDENCIA/ RIQUELME N 260 SANTIAGO   |  |                  |                                                                                       |
| EDIFICIO   |  |                  | LÁMINA                                                                                |
| RESIDENCIA UNIVERSITARIA   |  |                  | 1                                                                                     |
| MARIO OJEDA/ AMANDA LABARCA   |  |                  |                                                                                       |
| ORGANISMO   |  |                  | DE 1                                                                                  |
| Unidad de Gestión y Proyectos   |  |                  |                                                                                       |
| ROL SI   |  | DESTINO          | ESCALA                                                                                |
| 3505-1   |  | Habitacional     | 1:25                                                                                  |
| CONTENIDO   |  |                  |  |
| Mueblería a medida   |  |                  |                                                                                       |
| FECHA   |  | DIBUJADO POR     |                                                                                       |
| 25-06-2026   |  | Eduardo Rojas C. |                                                                                       |