



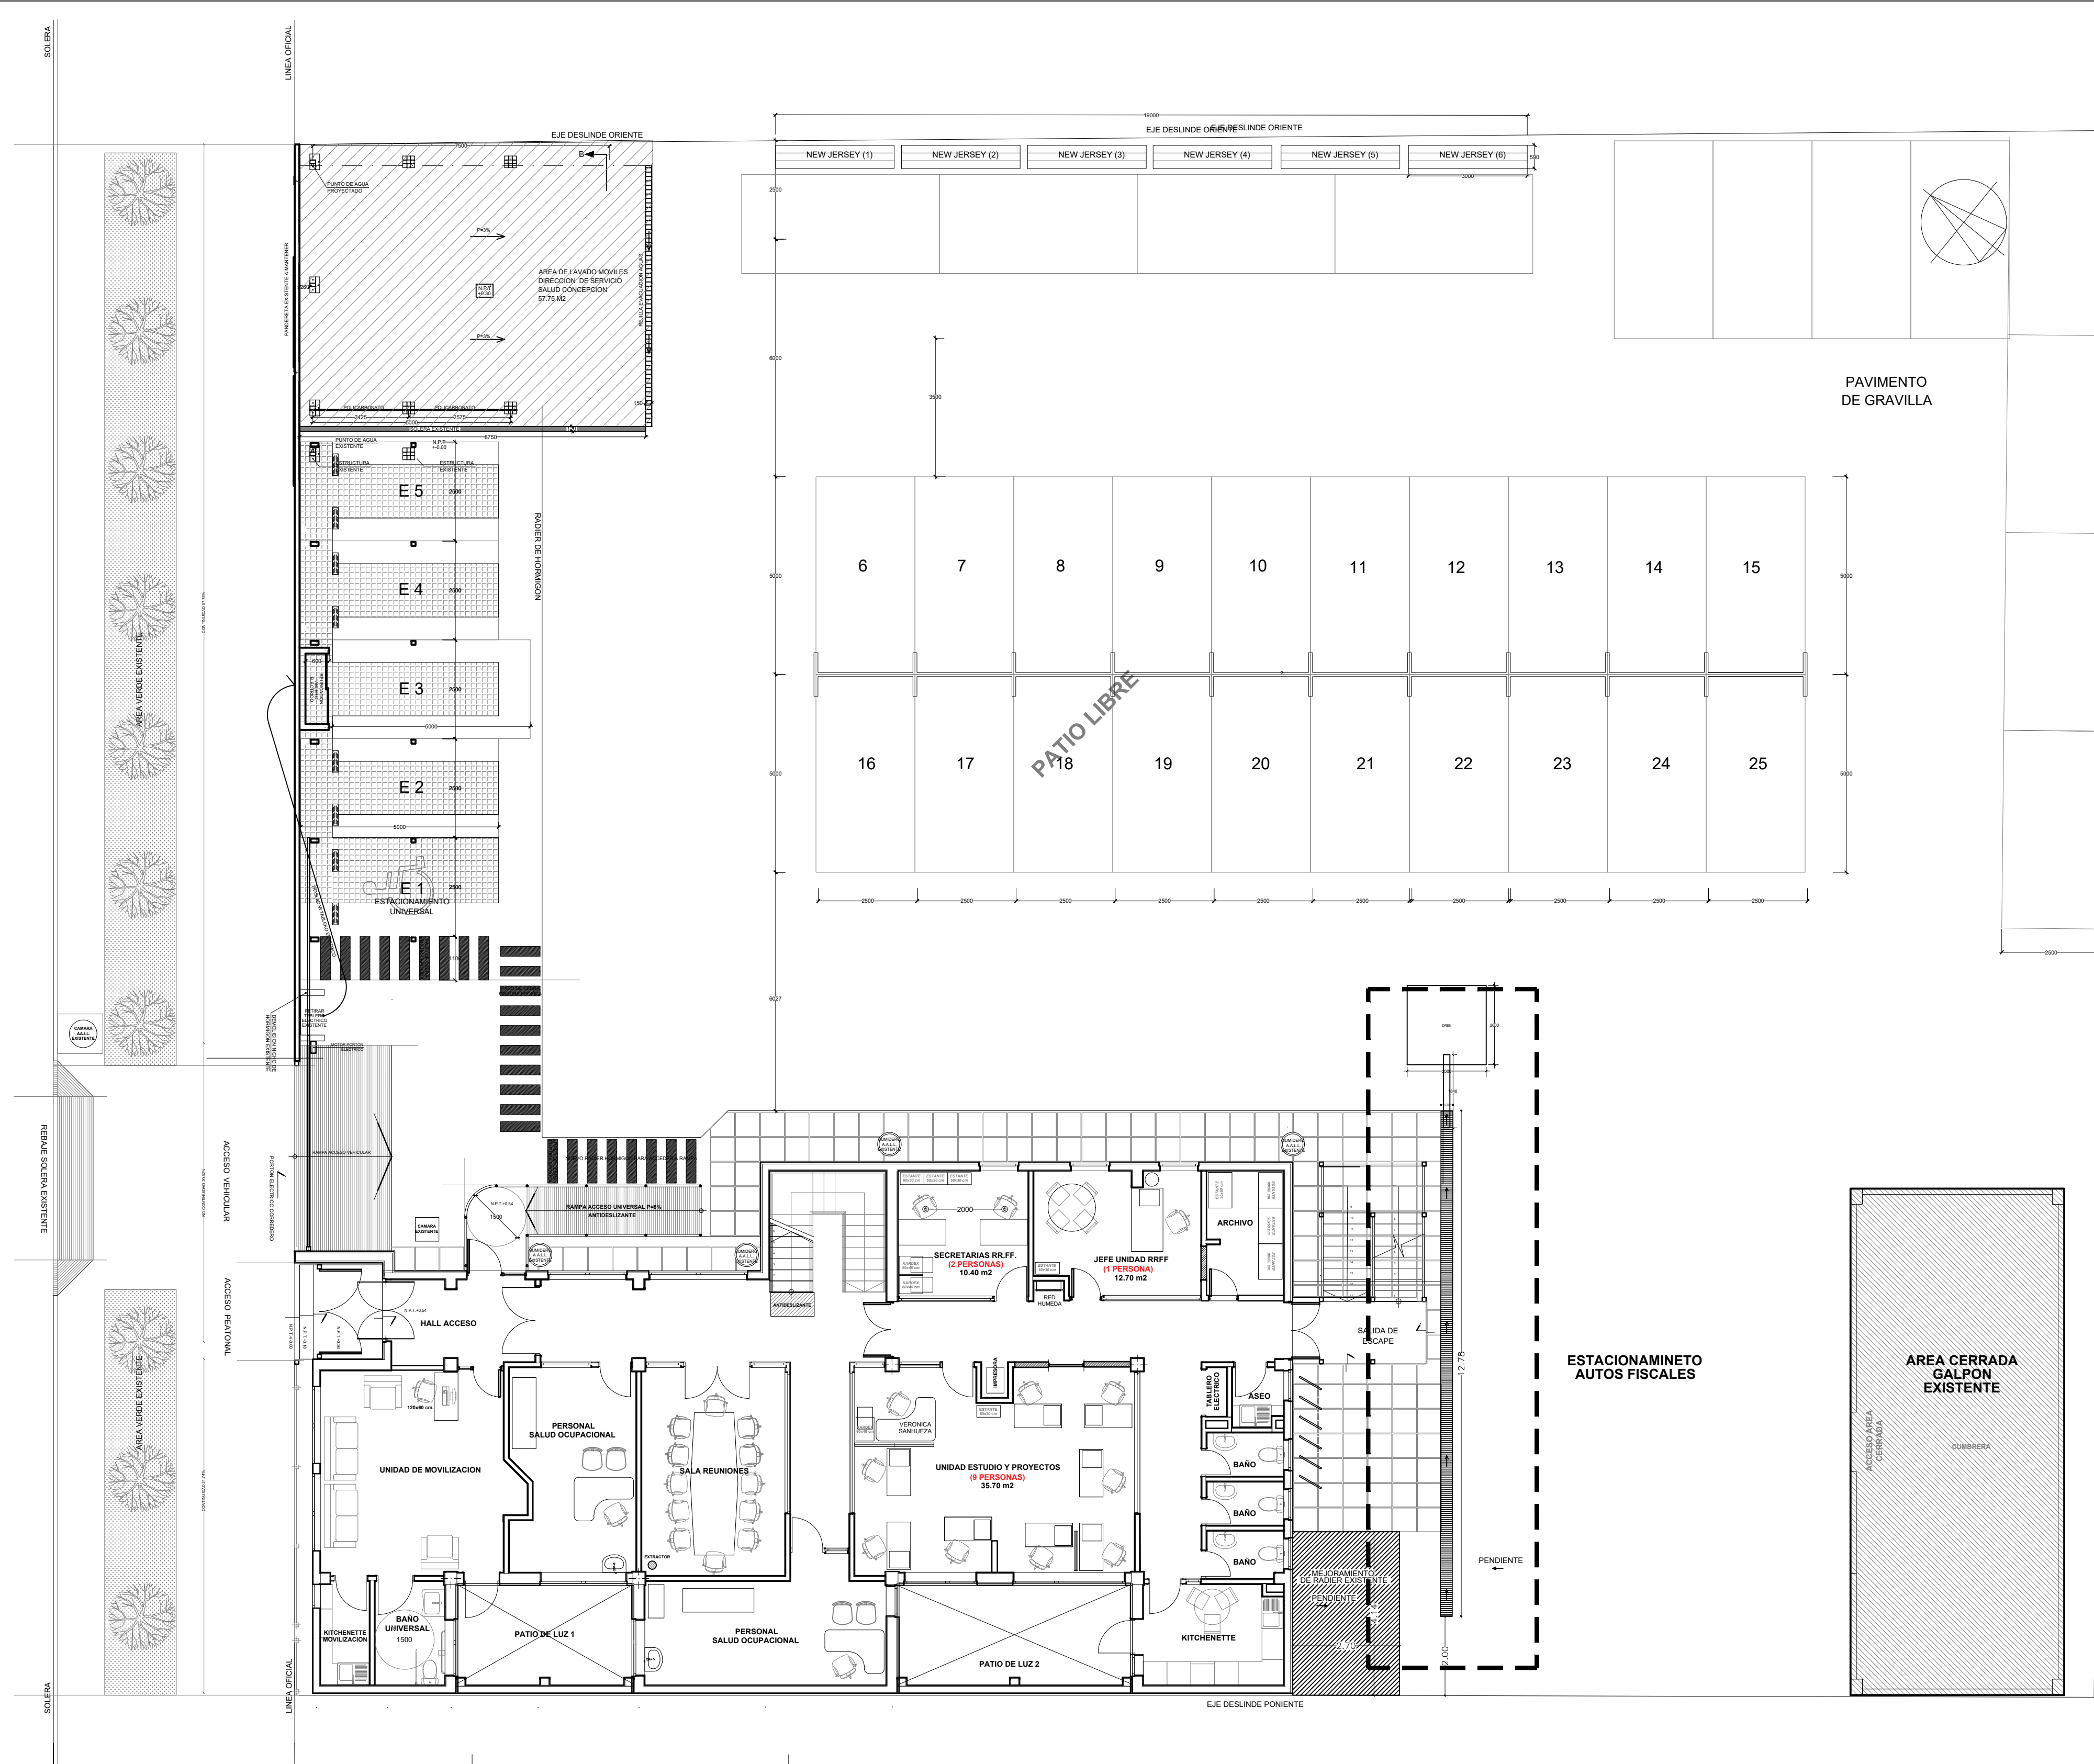

PLANTA DE ARQUITECTURA
ESC 1/100

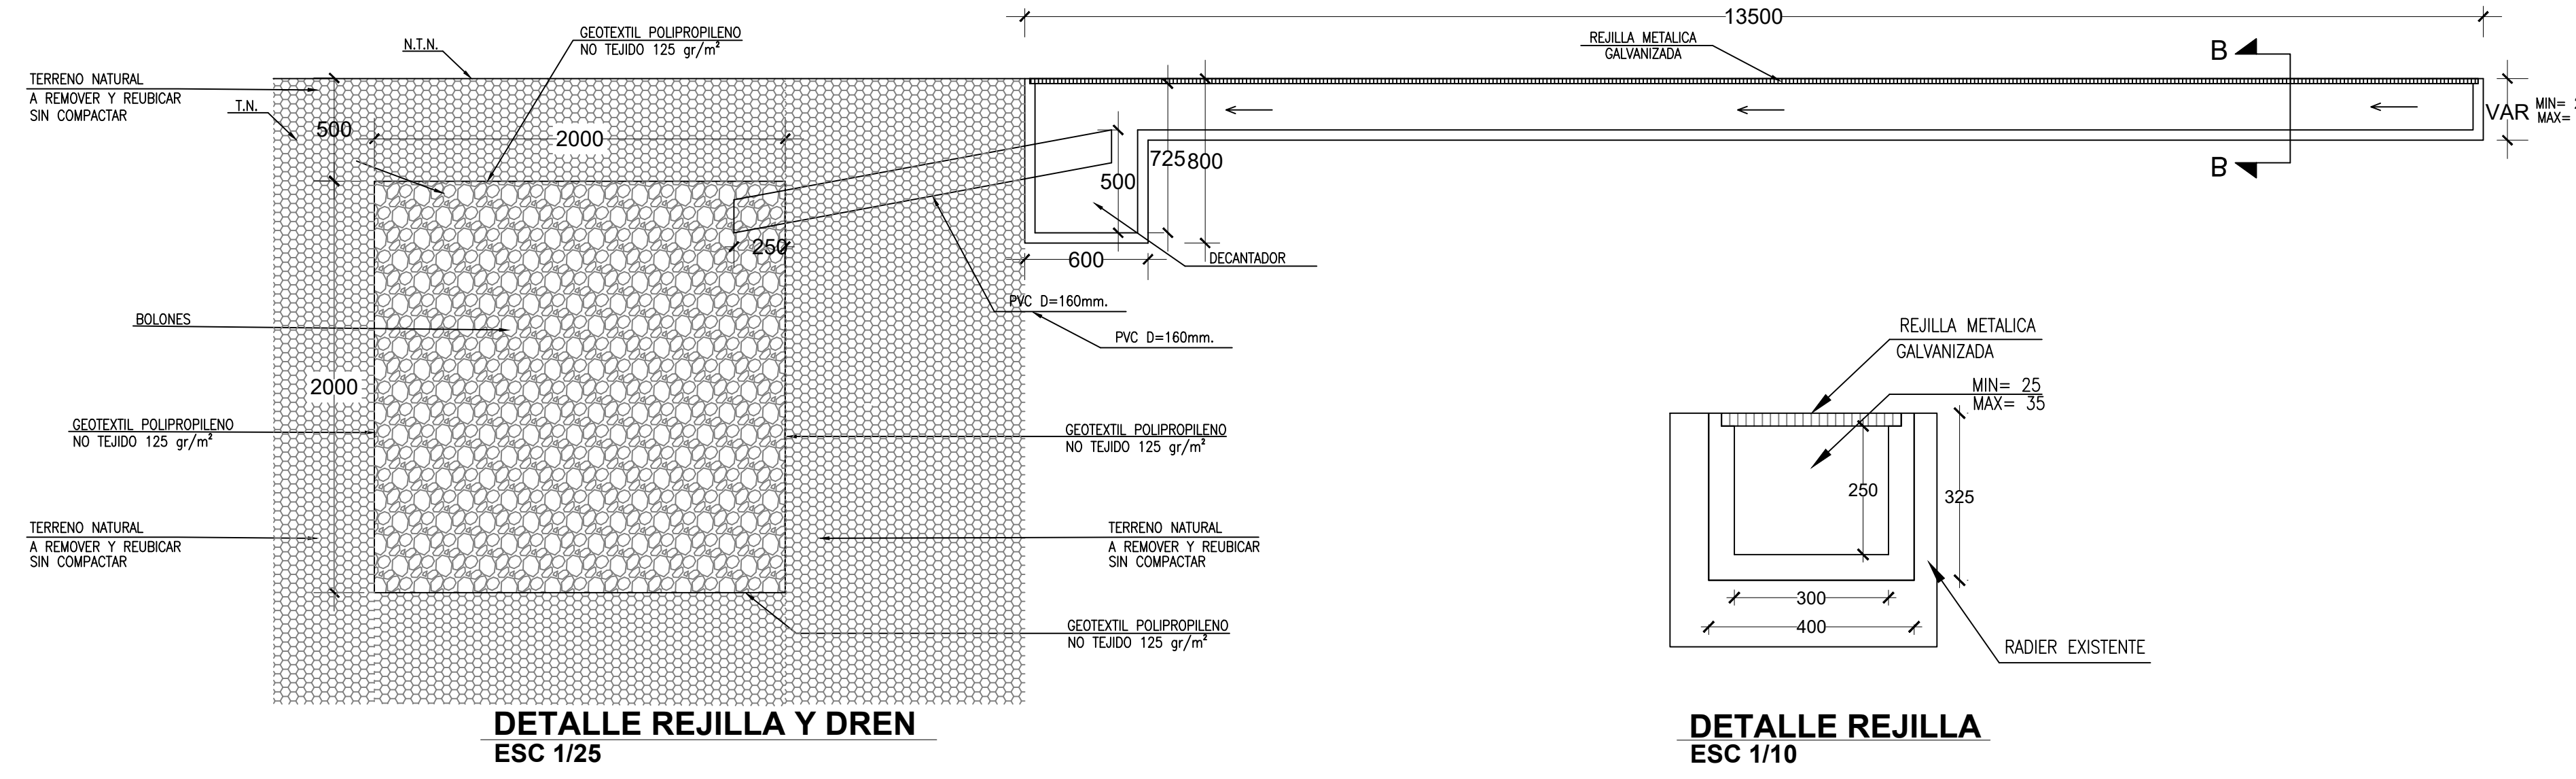

DETALLE REJILLA Y DREN
ESC 1/25

DETALLE REJILLA
ESC 1/10



Ministerio de Salud

DEPARTAMENTO DE RECURSOS FISICOS

PROYECTO:
SISTEMA EVACUACION DE AGUAS LLUVIAS
EDIFICIO OFICINAS
SERVICIO DE SALUD CONCEPCION

Dircción :
OHIGGINS 258
CONCEPCION-BIOBIO

SRA. ALEJANDRA BRAVO E.
Directora (a) Servicio Salud Concepción

SRA. ANDREA CATALAN V.
Subdirectora (a) IRMT Y Transmisión

SR. CHRISTIAN LAMA M.
Jefe (OS) de IRMT

Arquitecto:
JOHNNY VILLOUTA BUSTAMANTE

UBICACION:
LITONIO MAGALLANO
CALLE OHIGGINS 258
CALLE ALBA

Construcción Llamada:
IMPLEMENTACION REJILLA Y DREN
EVACUACION AGUAS LLUVIAS

Lámina:
SAN 01

Elaborado:
SANITARIO

Escala:
Como se indica

Fecha:
MAYO 2025

Revisado: