
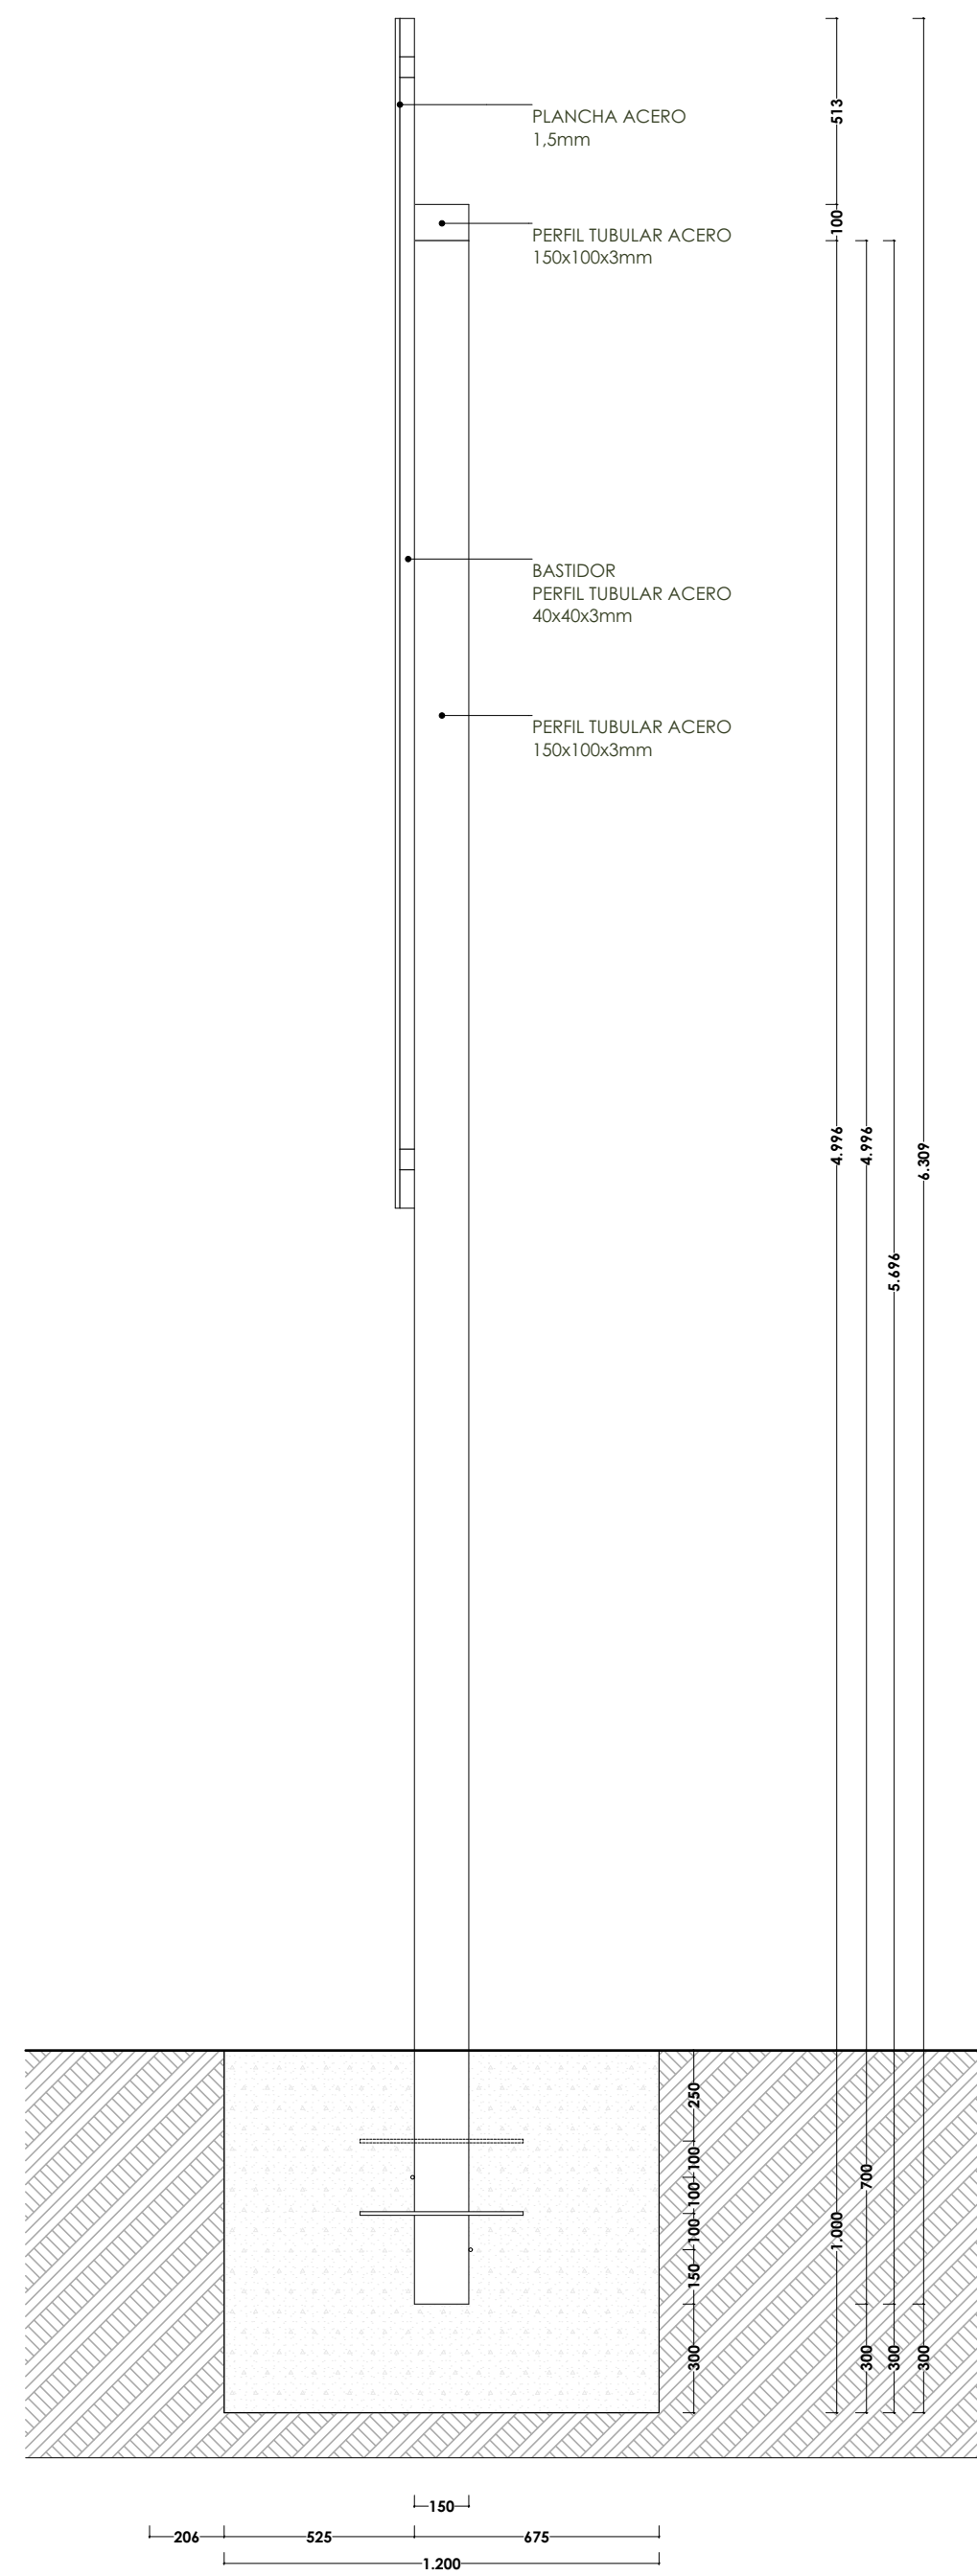



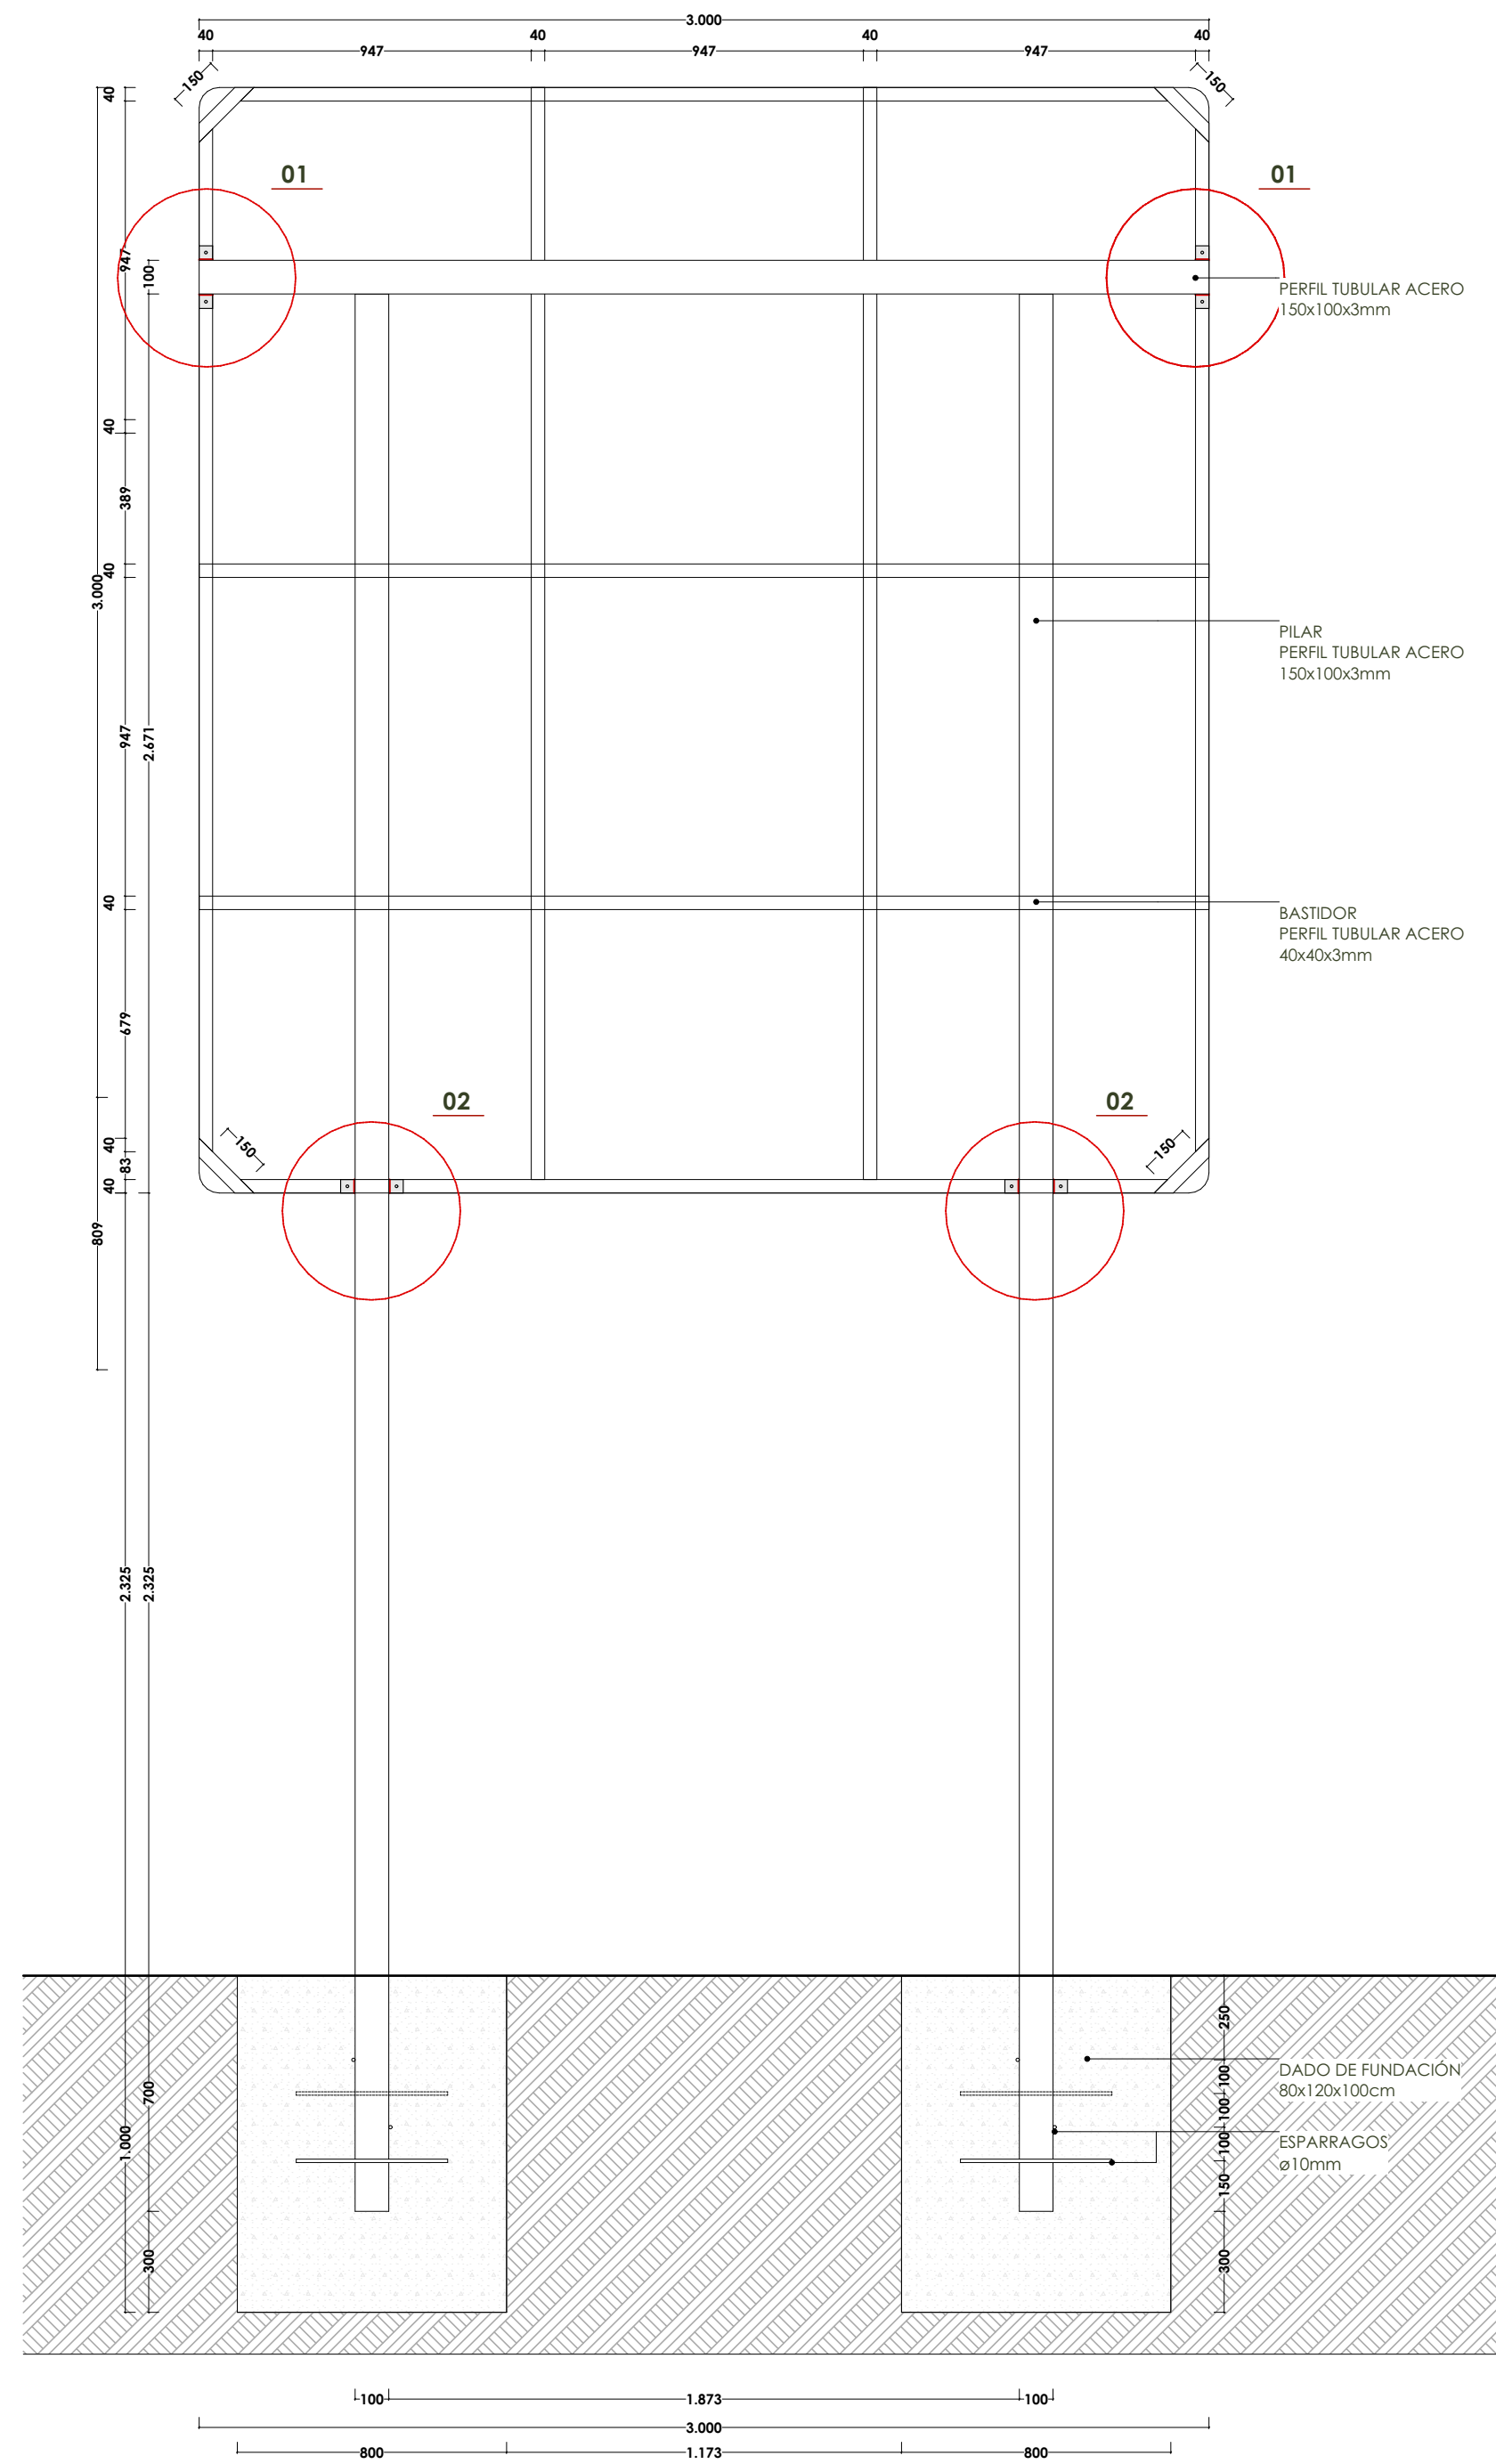


E01 | ELEVACIÓN FRONTAL COLOR 1:20

E01 | ELEVACIÓN FRONTAL 1:20

E01 | ELEVACIÓN POSTERIOR 1:20

E01 | ELEVACIÓN LATERAL 1:20

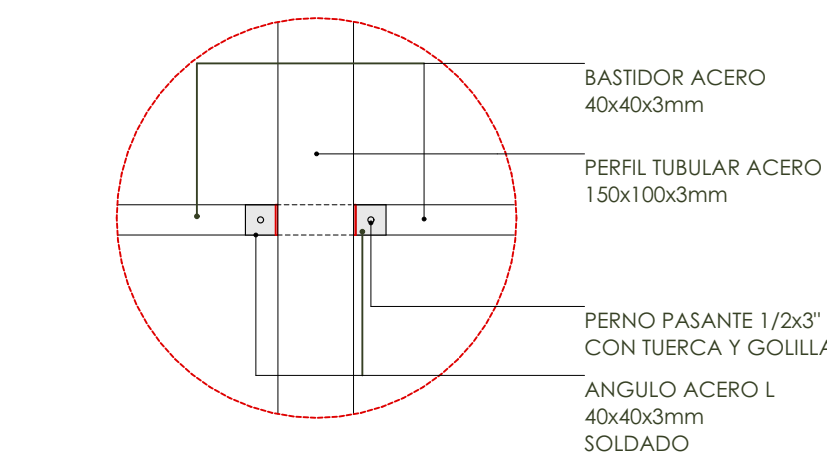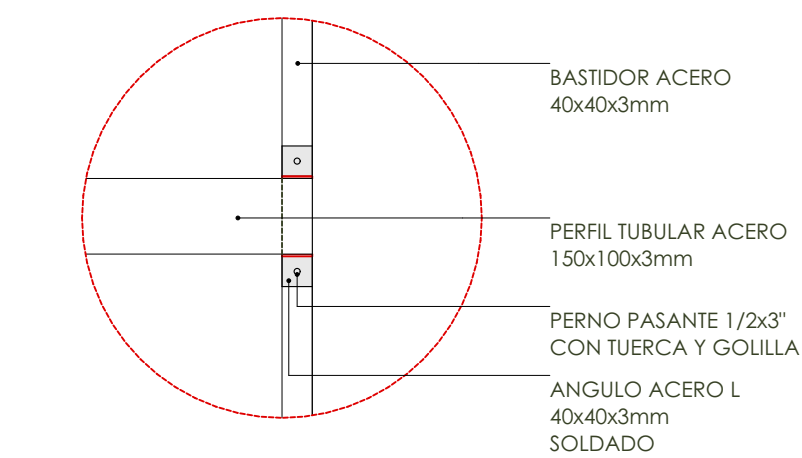

D01 | DETALLE UNIÓN ESTRUCTURA Y BASTIDOR 1:10

D02 | DETALLE UNIÓN ESTRUCTURA Y BASTIDOR 1:10

LETRERO INTERES TURISTICO

Dirección	S/D
ROL	S/R
Ciudad	Dalcahue
Provincia	Chiloé

Nombre del Dibujo
PLANIMETRIA LETRERO

Propietario: Ilustre Municipalidad de Dalcahue