

PROPIEDAD SURALIS S.A.
ROL 02914-00057

ESTERILIZACIÓN CANINA
MUNICIPAL
ROL 02914-00056

PROPIEDAD SURALIS S.A.

PROPIEDAD SURALIS S.A.
ROL 02141-00212

PROPIEDAD MUNICIPAL
ROL 02141-00195
5.667,86 m²

STRIP CENTER CENTRO COMERCIAL MUNITA
PROPIEDAD ELENA JARAMILLO

AV. SARGENTO SILVA

INTERSECCIÓN EJES	COORDENADA UTM (E)	COORDENADA UTM (N)
A1	672351,2129	5408814,447
A2	672350,067	5408815,322
B1	672350,3181	5408813,274
B2	672349,1722	5408814,149
C1	672349,4232	5408812,102
C2	672348,2773	5408812,976



CONSTRUCCIÓN LETRERO INFORMATIVO
CECOSF LAWÉN
compra ágil


UBICACIÓN

Av. Sargento Silva, Puerto Montt, Los Lagos

CONTENIDO LÁMINA

Planimetría emplazamiento, Tabla de coordenadas 1:250

CÓDIGO	LÁMINA	ESCALAS	FECHA
	L.01	1:250	25-09-2026
DIBUJO		ARCHIVO DIGITAL	
FRA.		CECOSF Lawén-Letrero proyecto_Rev.00.pln	

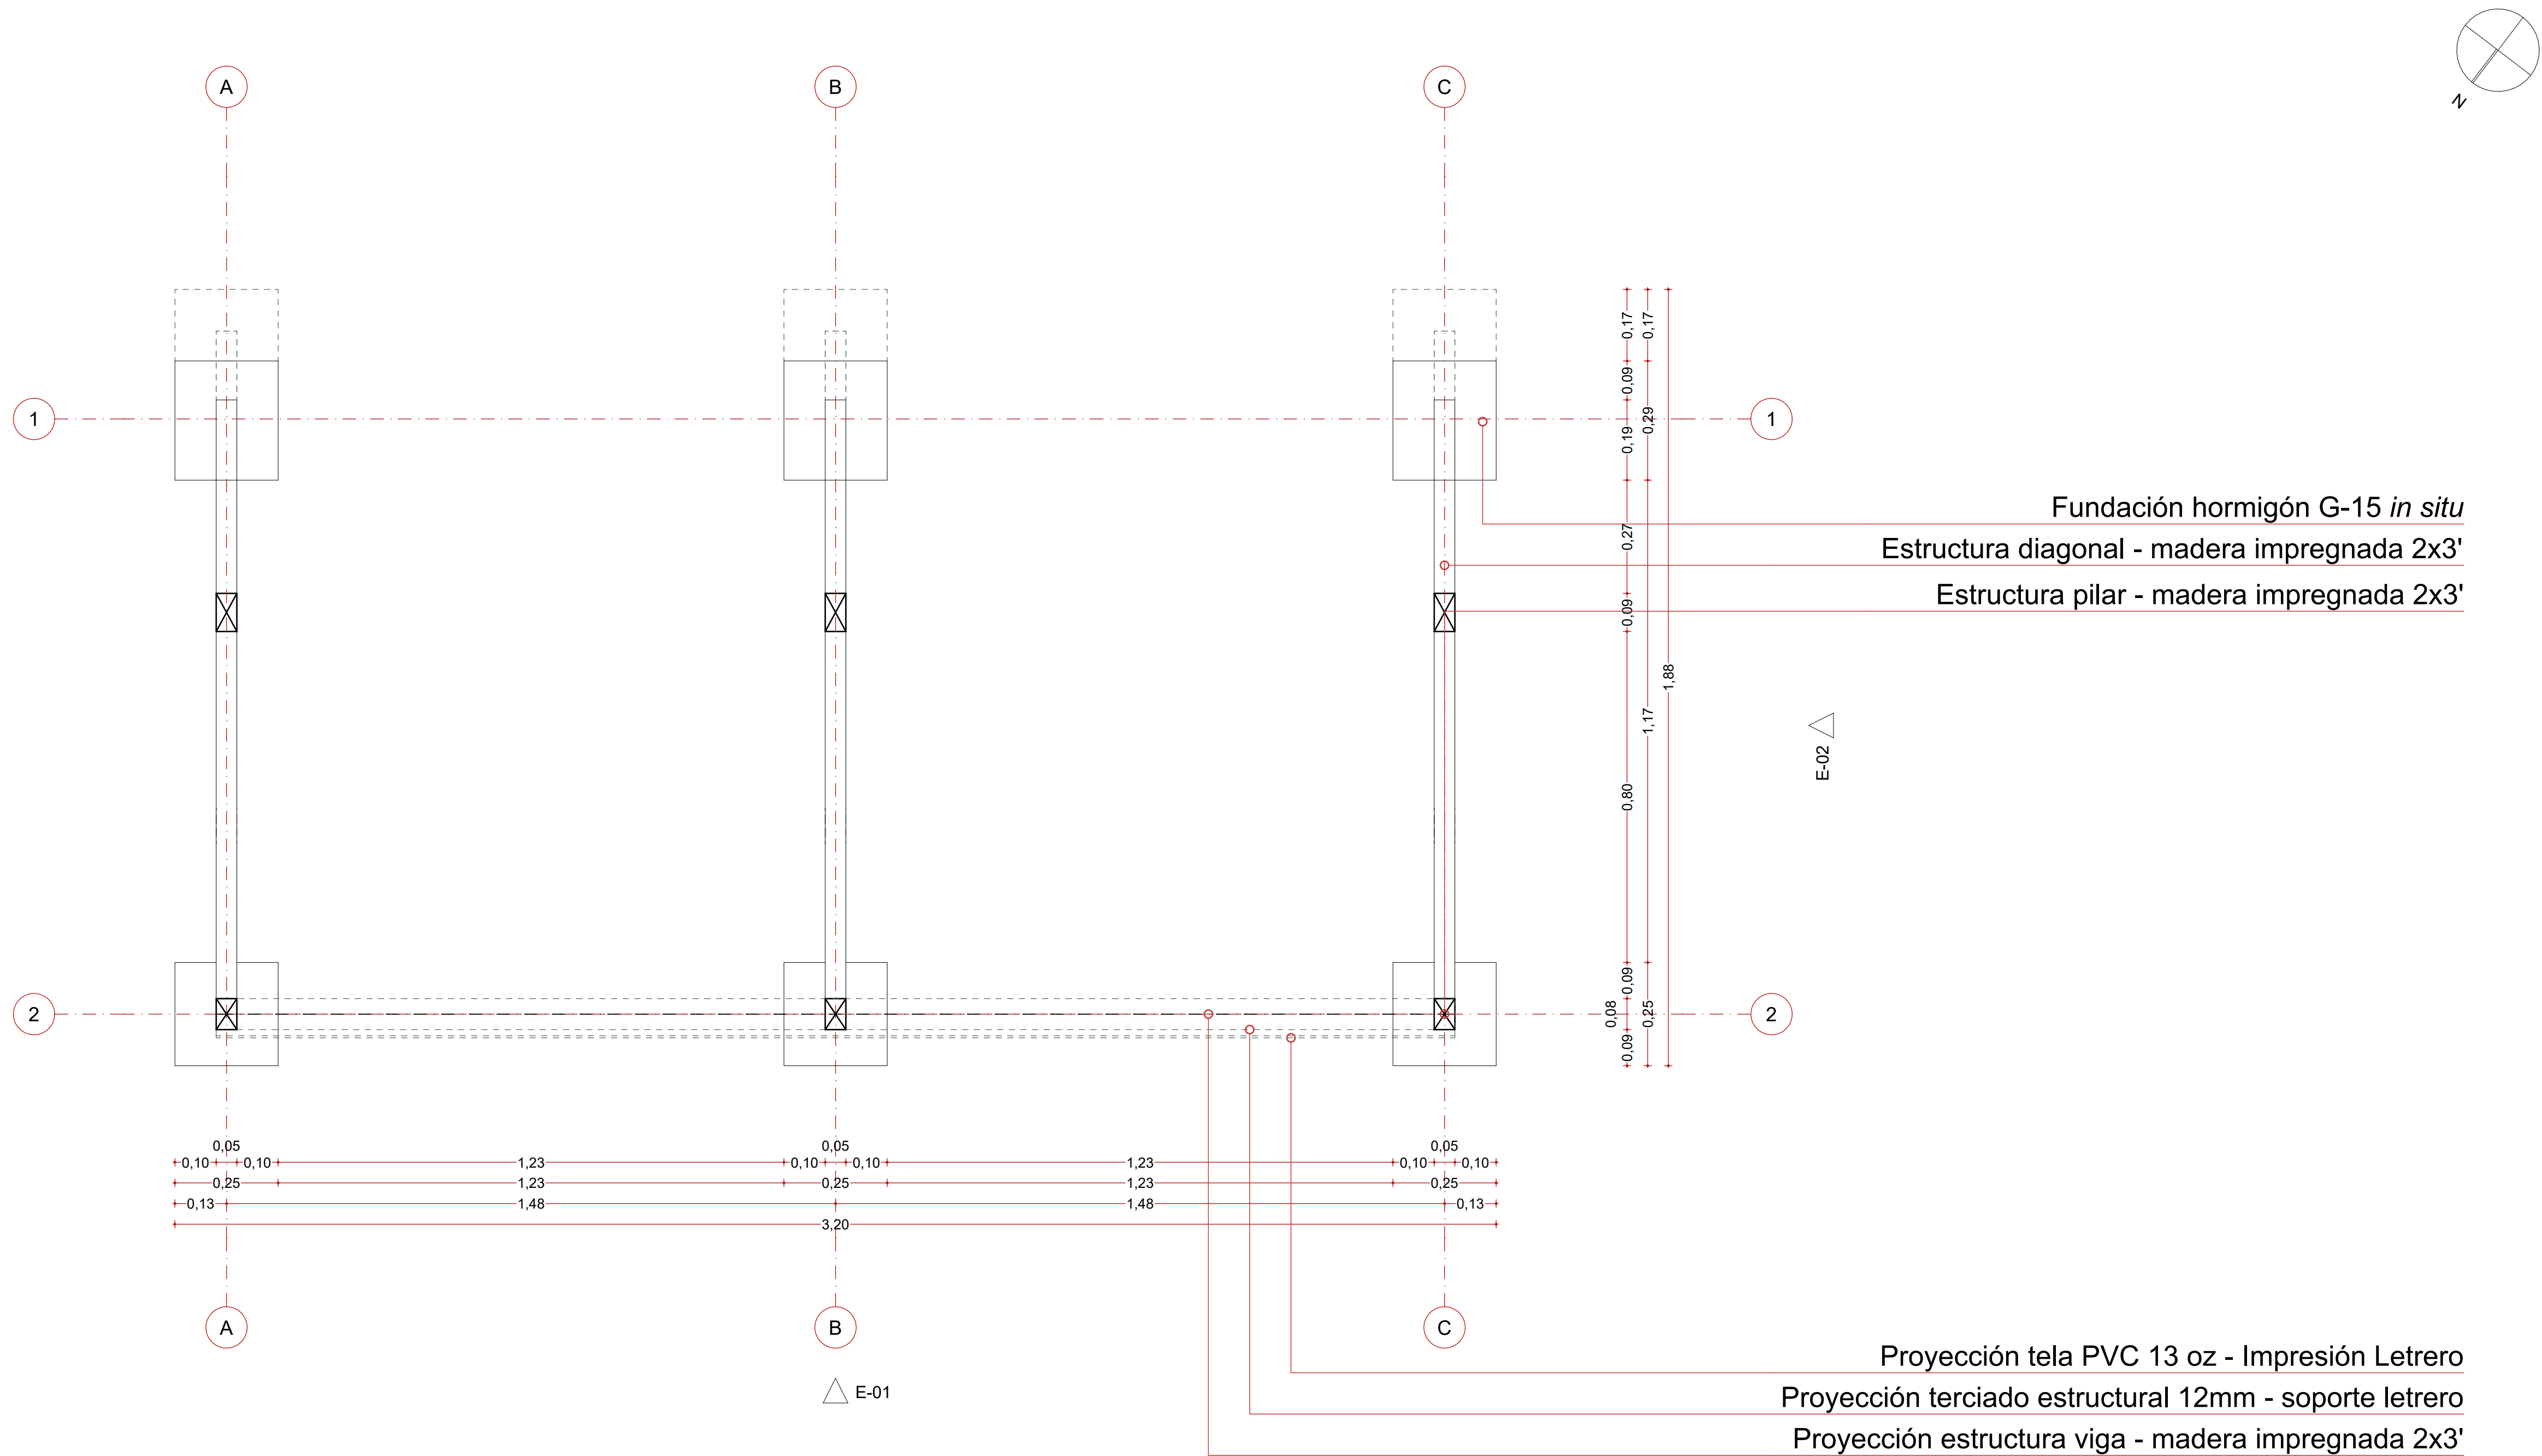

CONSTRUCCIÓN LETRERO INFORMATIVO
CECOSF LAWÉN
compra ágil


UBICACIÓN
Av. Sargento Silva, Puerto Montt, Los Lagos

CONTENIDO LÁMINA
Planimetría 1:10

CÓDIGO	LÁMINA	ESCALAS	FECHA
	L. 02	1:10	25-09-2026

DIBUJÓ
FRA.

ARCHIVO DIGITAL
CECOSF Lawén-Letrero proyecto_Rev.00.pln

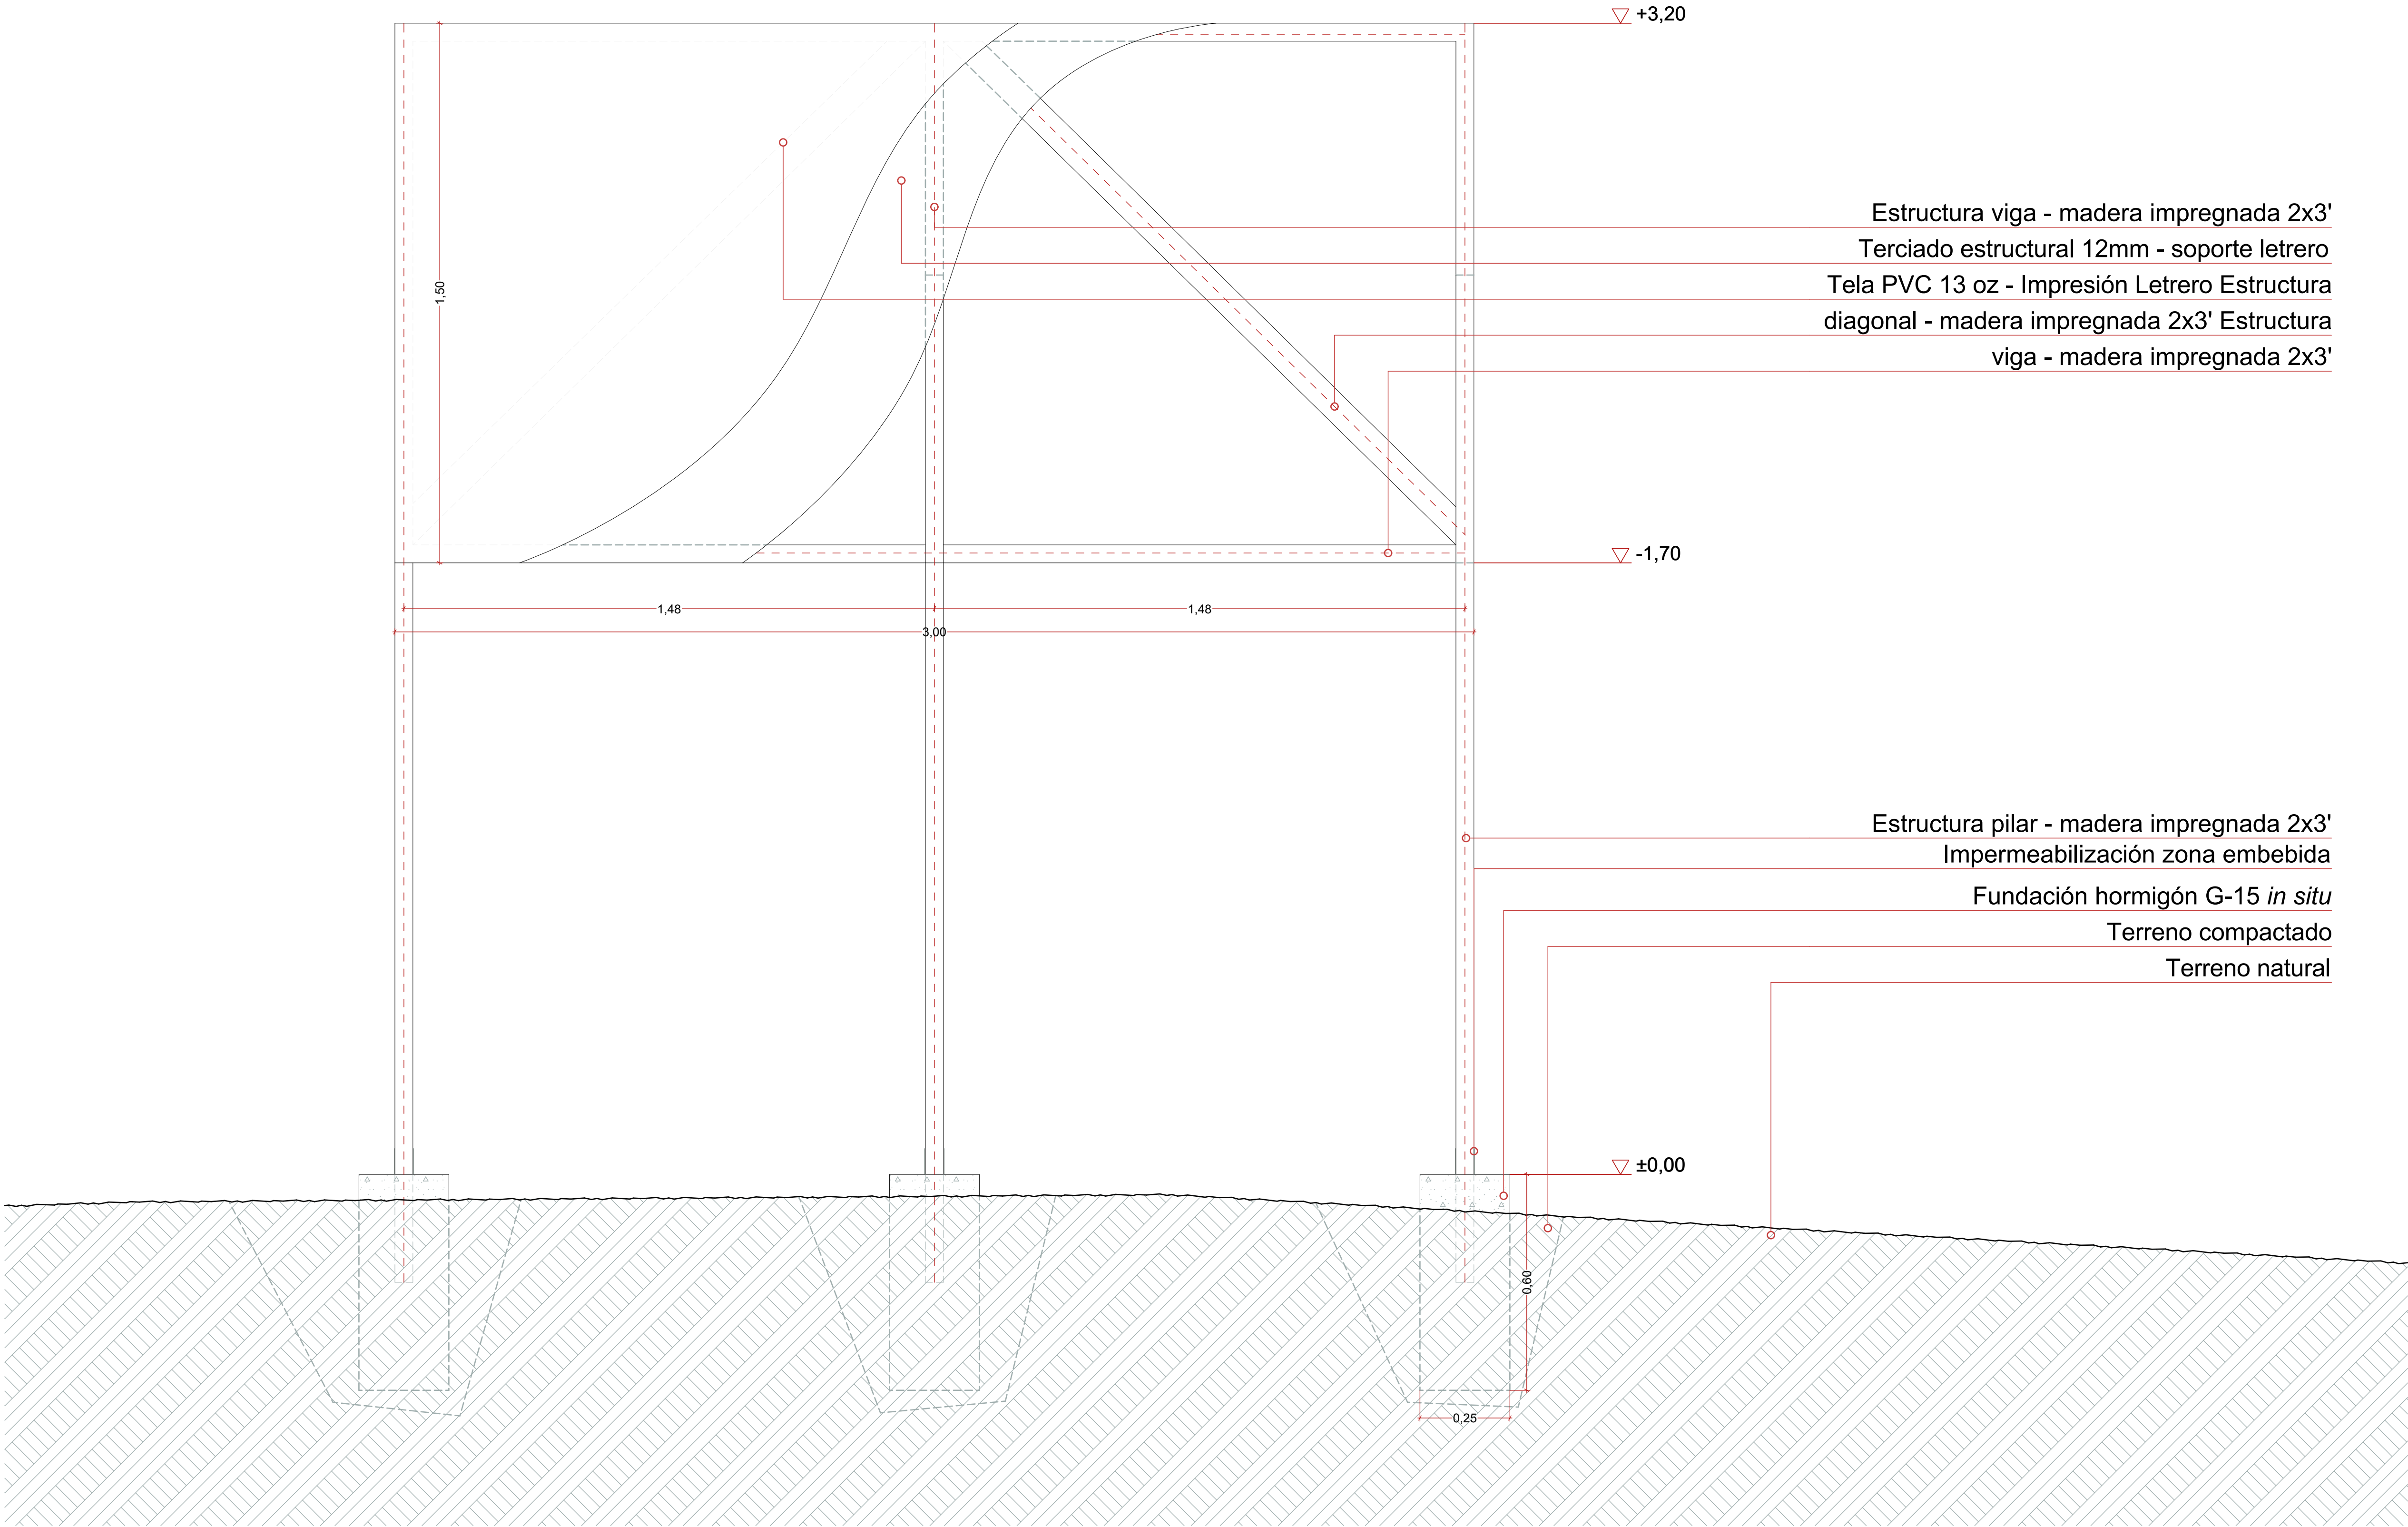




CONSTRUCCIÓN LETRERO INFORMATIVO
CECOSF LAWÉN
compra ágil

UBICACIÓN			
Av. Sargento Silva, Puerto Montt, Los Lagos			
CONTENIDO LÁMINA			
Elevación frontal		1:10	

CÓDIGO	LÁMINA	ESCALAS	FECHA
	L.03	1:10	25-09-2026

DIBUJÓ	ARCHIVO DIGITAL
FRA.	CECOSF Lawén-Letrero proyecto_Rev.00.pln

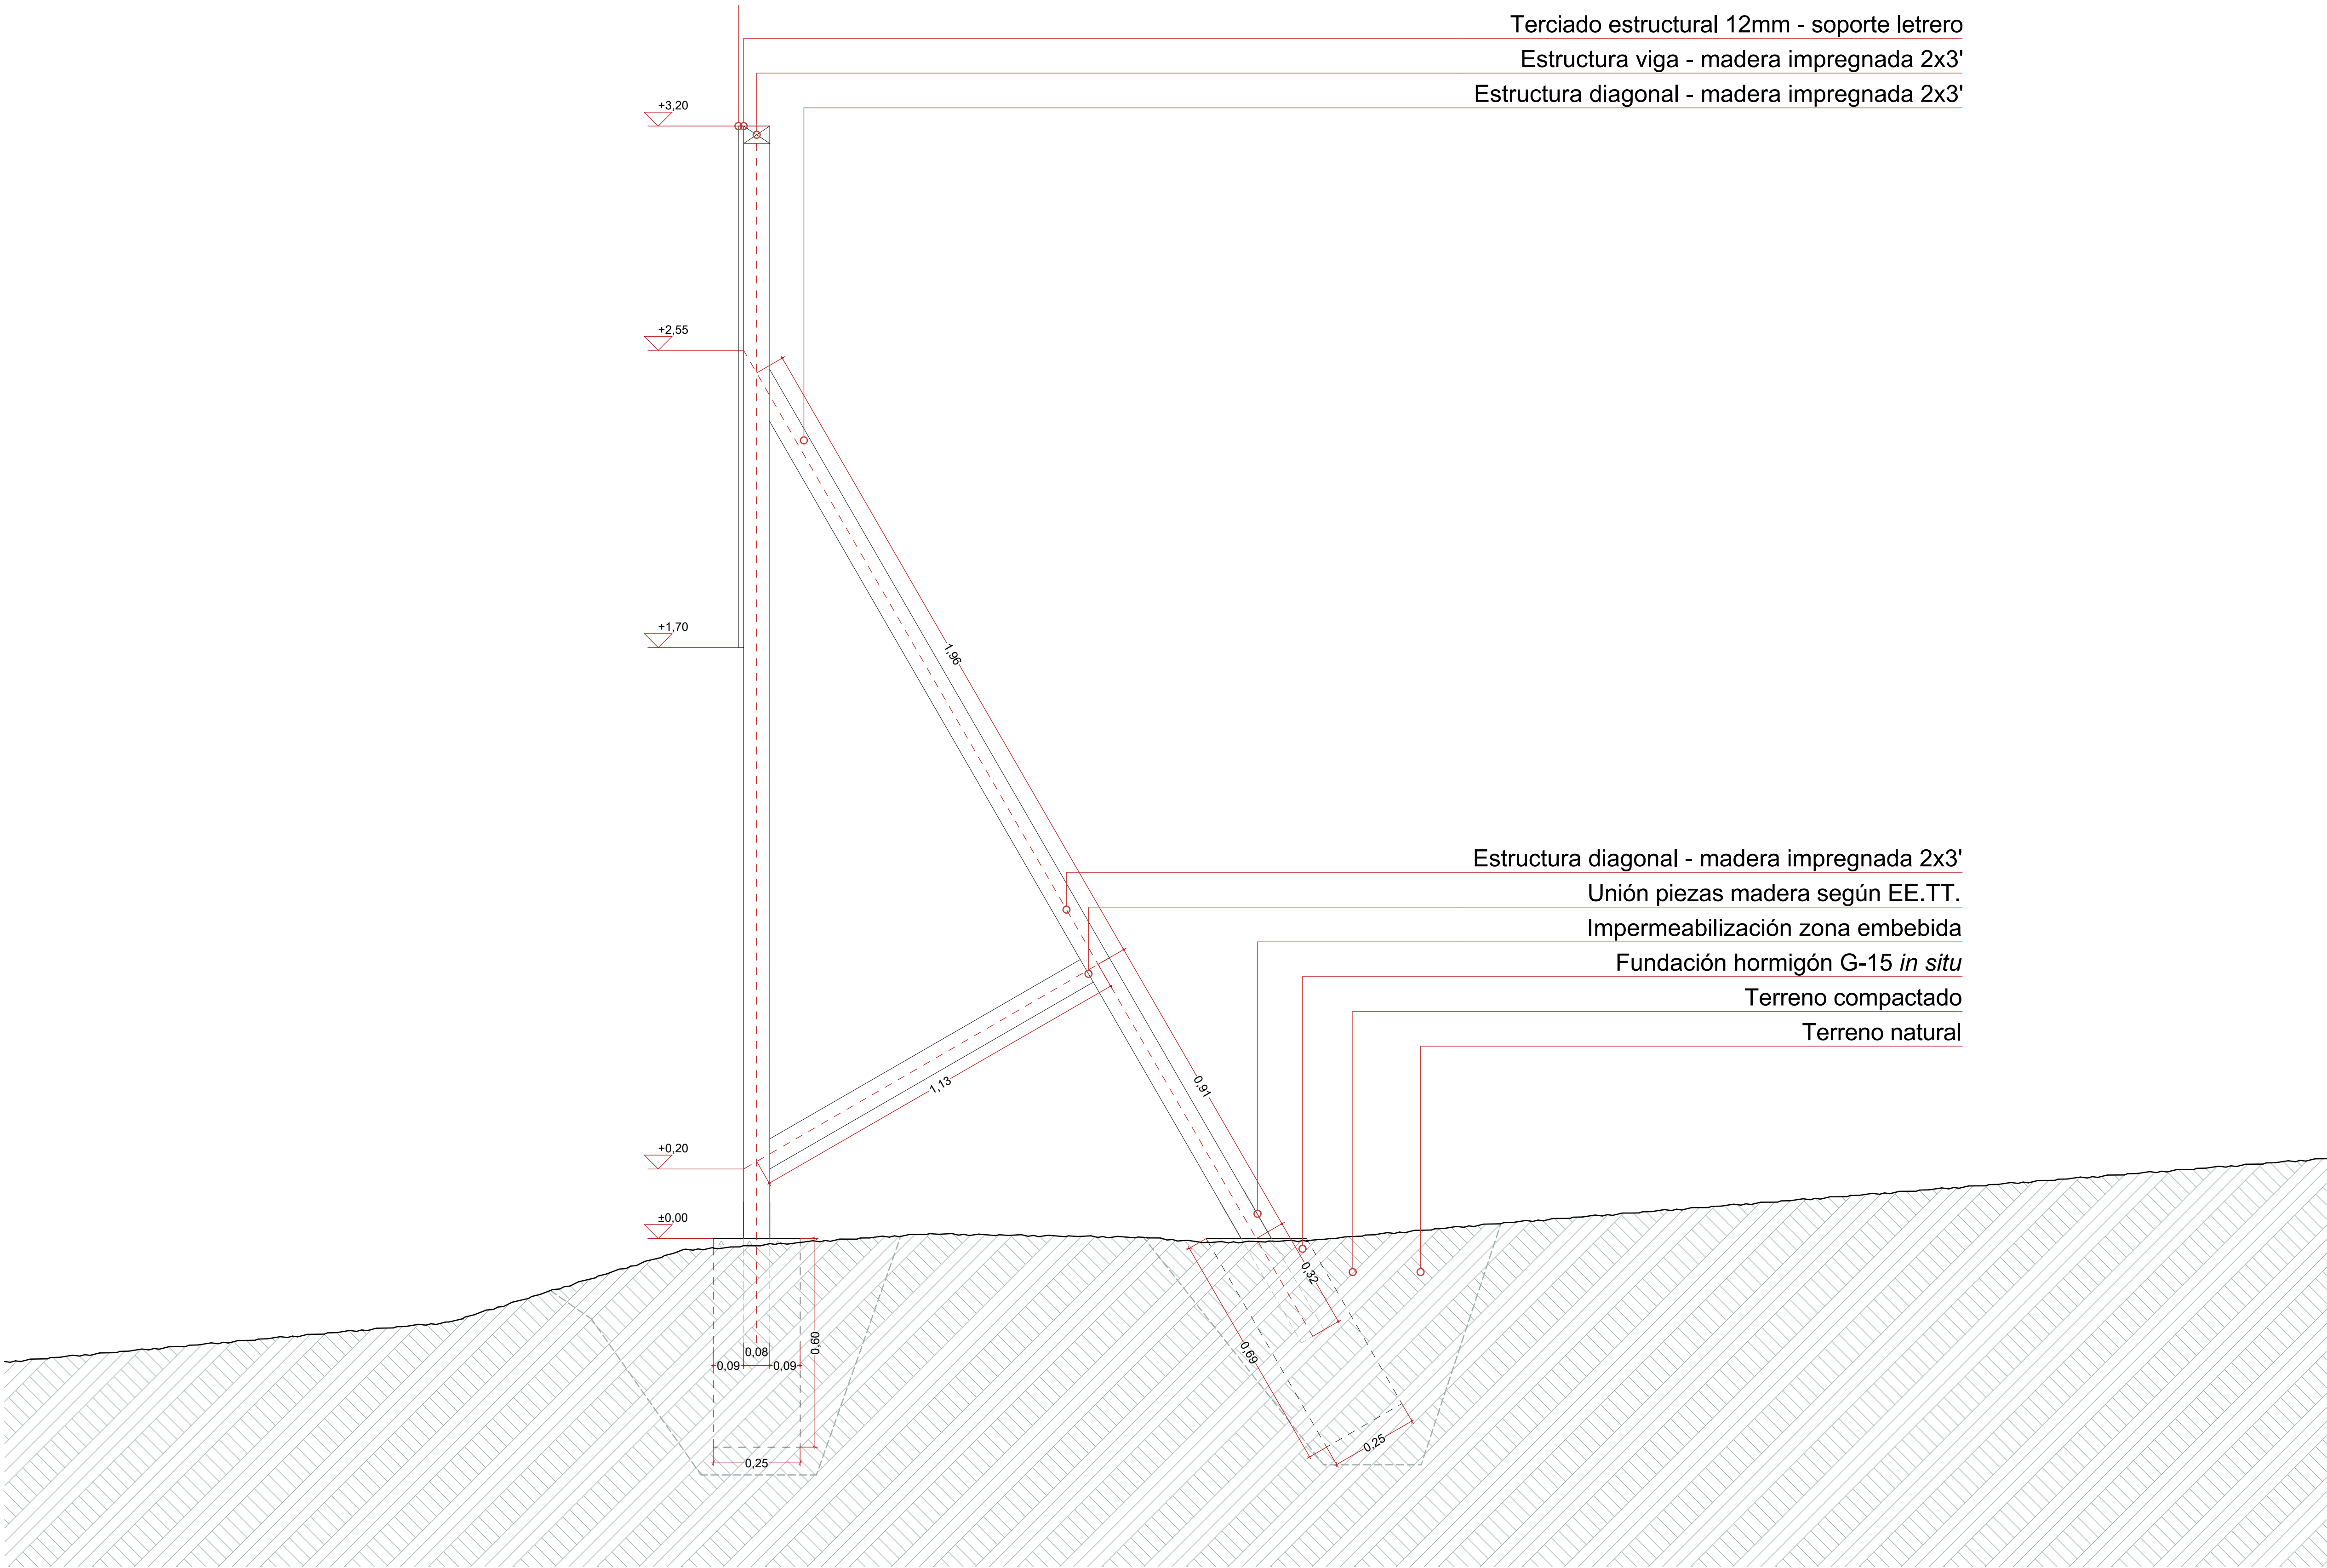

CONSTRUCCIÓN LETRERO INFORMATIVO
CECOSF LAWÉN
compra ágil


UBICACIÓN

Av. Sargento Silva, Puerto Montt, Los Lagos

CONTENIDO LÁMINA

Elevación lateral 1:10

CÓDIGO	LÁMINA	ESCALAS	FECHA
	L.04	1:10	25-09-2026
DIBUJÓ		ARCHIVO DIGITAL	
FRA.		CECOSF Lawén-Letrero proyecto_Rev.00.pln	

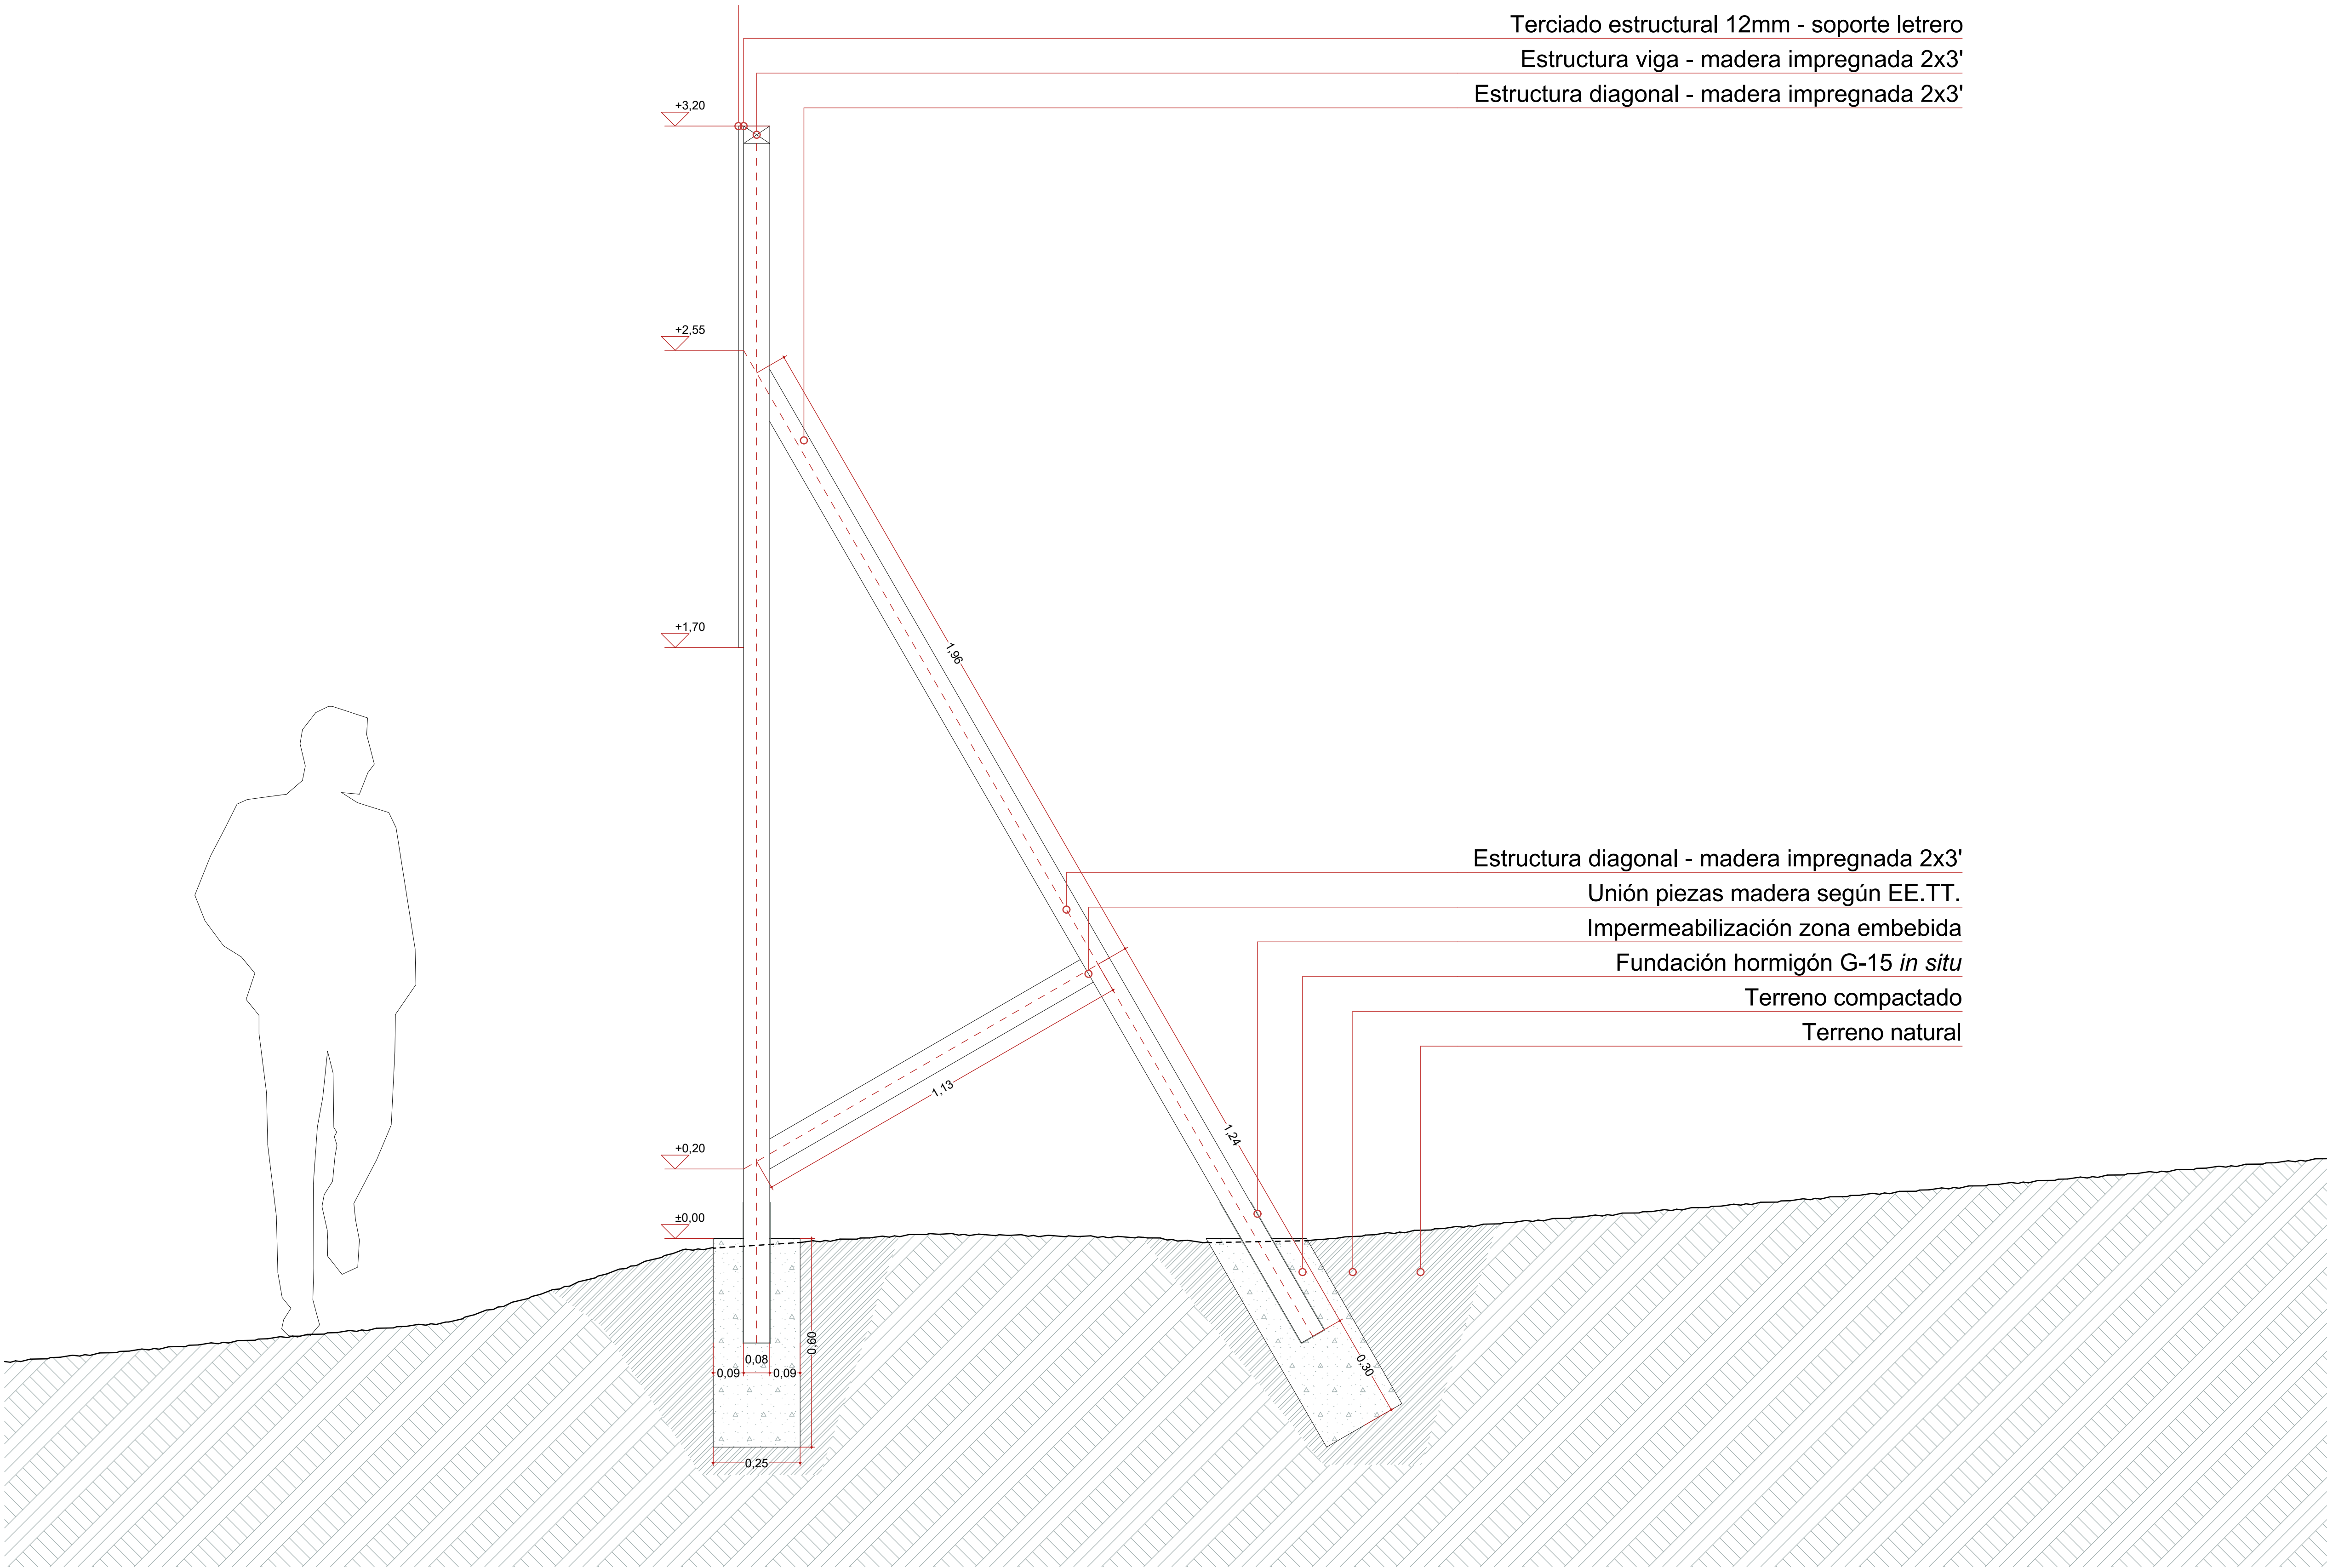



DESAM
DEPARTAMENTO DE
SALUD MUNICIPAL

CONSTRUCCIÓN LETRERO INFORMATIVO
CECOSF LAWÉN
compra ágil

UBICACIÓN

Av. Sargento Silva, Puerto Montt, Los Lagos

CONTENIDO LÁMINA

Corte eje C1:10


CÓDIGO	LÁMINA	ESCALAS	FECHA
	L.05	1:10	25-09-2026

DIBUJÓ

ARCHIVO DIGITAL

FRA.

CECOSF Lawén-Letrero proyecto_Rev.00.pln

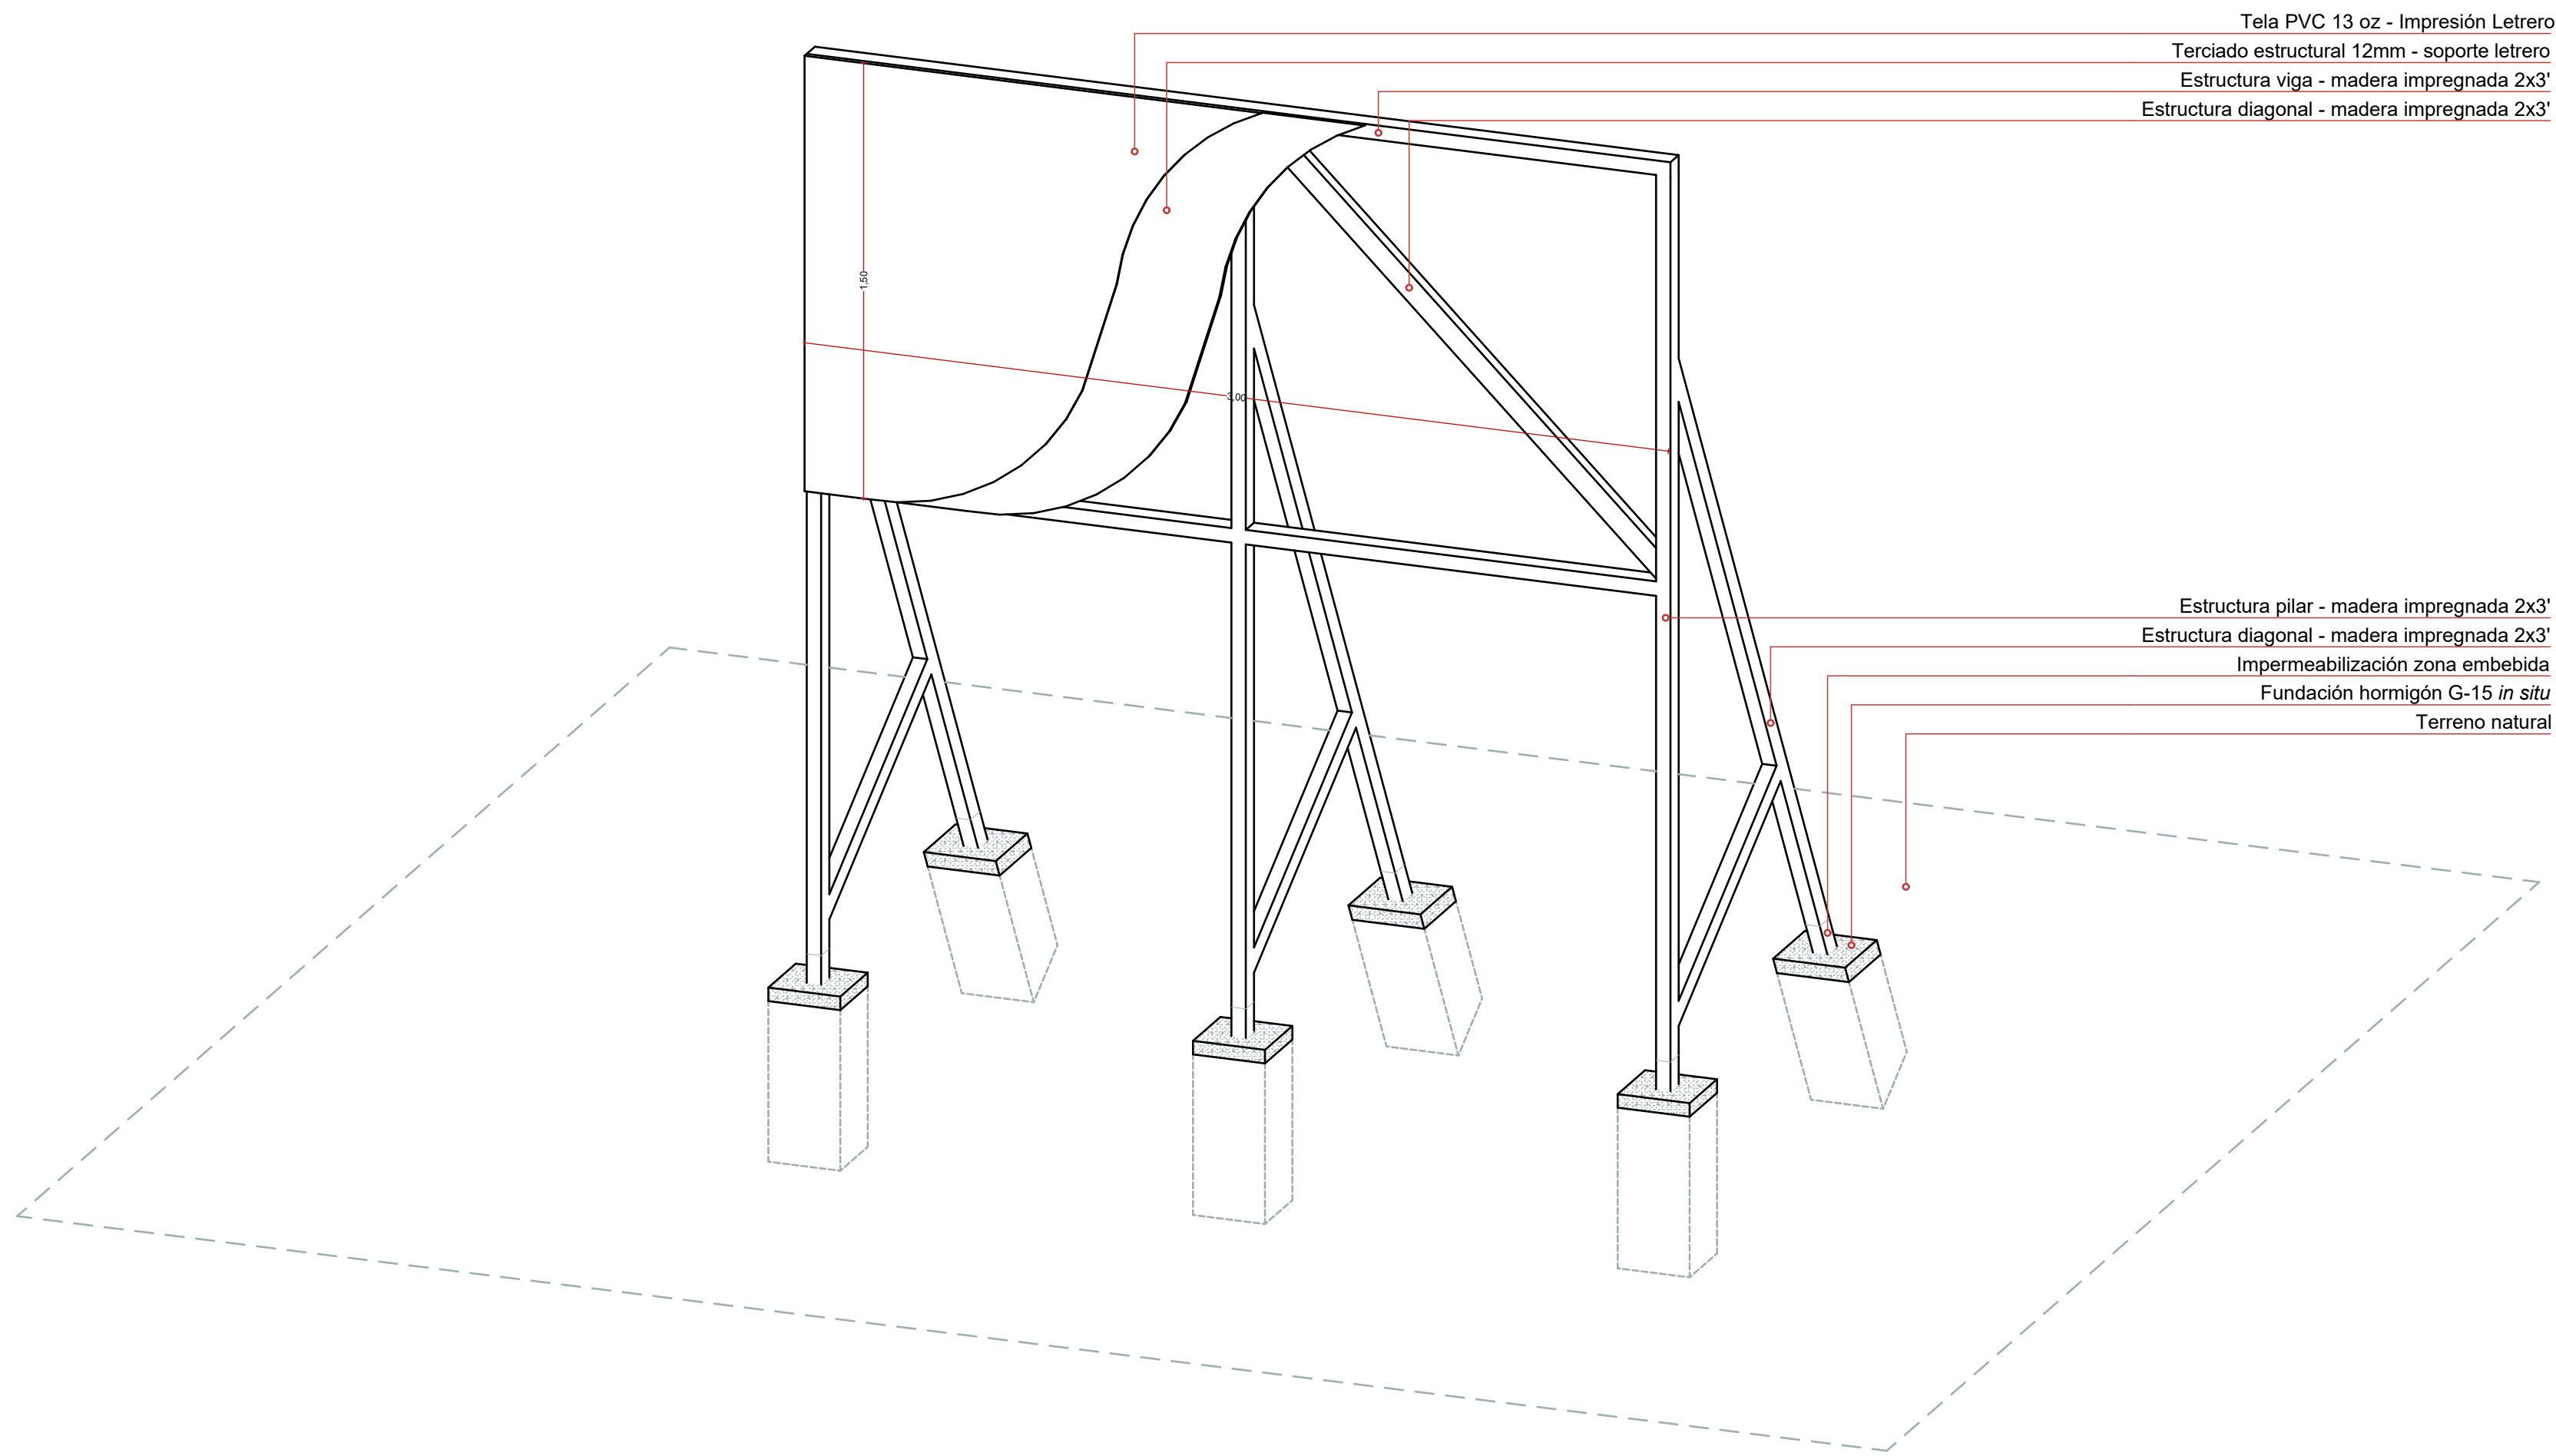

3D-01

Diagrama axonométrica

1:20



L-01

Diseño letrero

  DESAM DEPARTAMENTO DE SALUD MUNICIPAL											
CONSTRUCCIÓN LETRERO INFORMATIVO CECOSF LAWÉN compra ágil											
UBICACIÓN Av. Sargento Silva, Puerto Montt, Los Lagos											
CONTENIDO LÁMINA Diagrama axonométrica, Diseño letrero 1:20											
<table> <tr> <th>CÓDIGO</th><th>LÁMINA</th><th>ESCALAS</th><th>FECHA</th></tr> <tr> <td></td><td>L.06</td><td>1:20</td><td>25-09-2026</td></tr> </table>				CÓDIGO	LÁMINA	ESCALAS	FECHA		L.06	1:20	25-09-2026
CÓDIGO	LÁMINA	ESCALAS	FECHA								
	L.06	1:20	25-09-2026								
DIBUJO FRA. ARCHIVO DIGITAL CECOSF Lawén-Letrero proyecto_Rev.00.pln											





DESAM
DEPARTAMENTO DE
SALUD MUNICIPAL

CONSTRUCCIÓN LETRERO INFORMATIVO
CECOSF LAWÉN
compra ágil

UBICACIÓN

Av. Sargento Silva, Puerto Montt, Los Lagos

CONTENIDO LÁMINA

Imagen objetivo1:1

CÓDIGO	LÁMINA	ESCALAS	FECHA
	L.07	1:1	25-09-2026

DIBUJO

ARCHIVO DIGITAL

FRA.

CECOSF Lawén-Letrero proyecto_Rev.00.pjn