
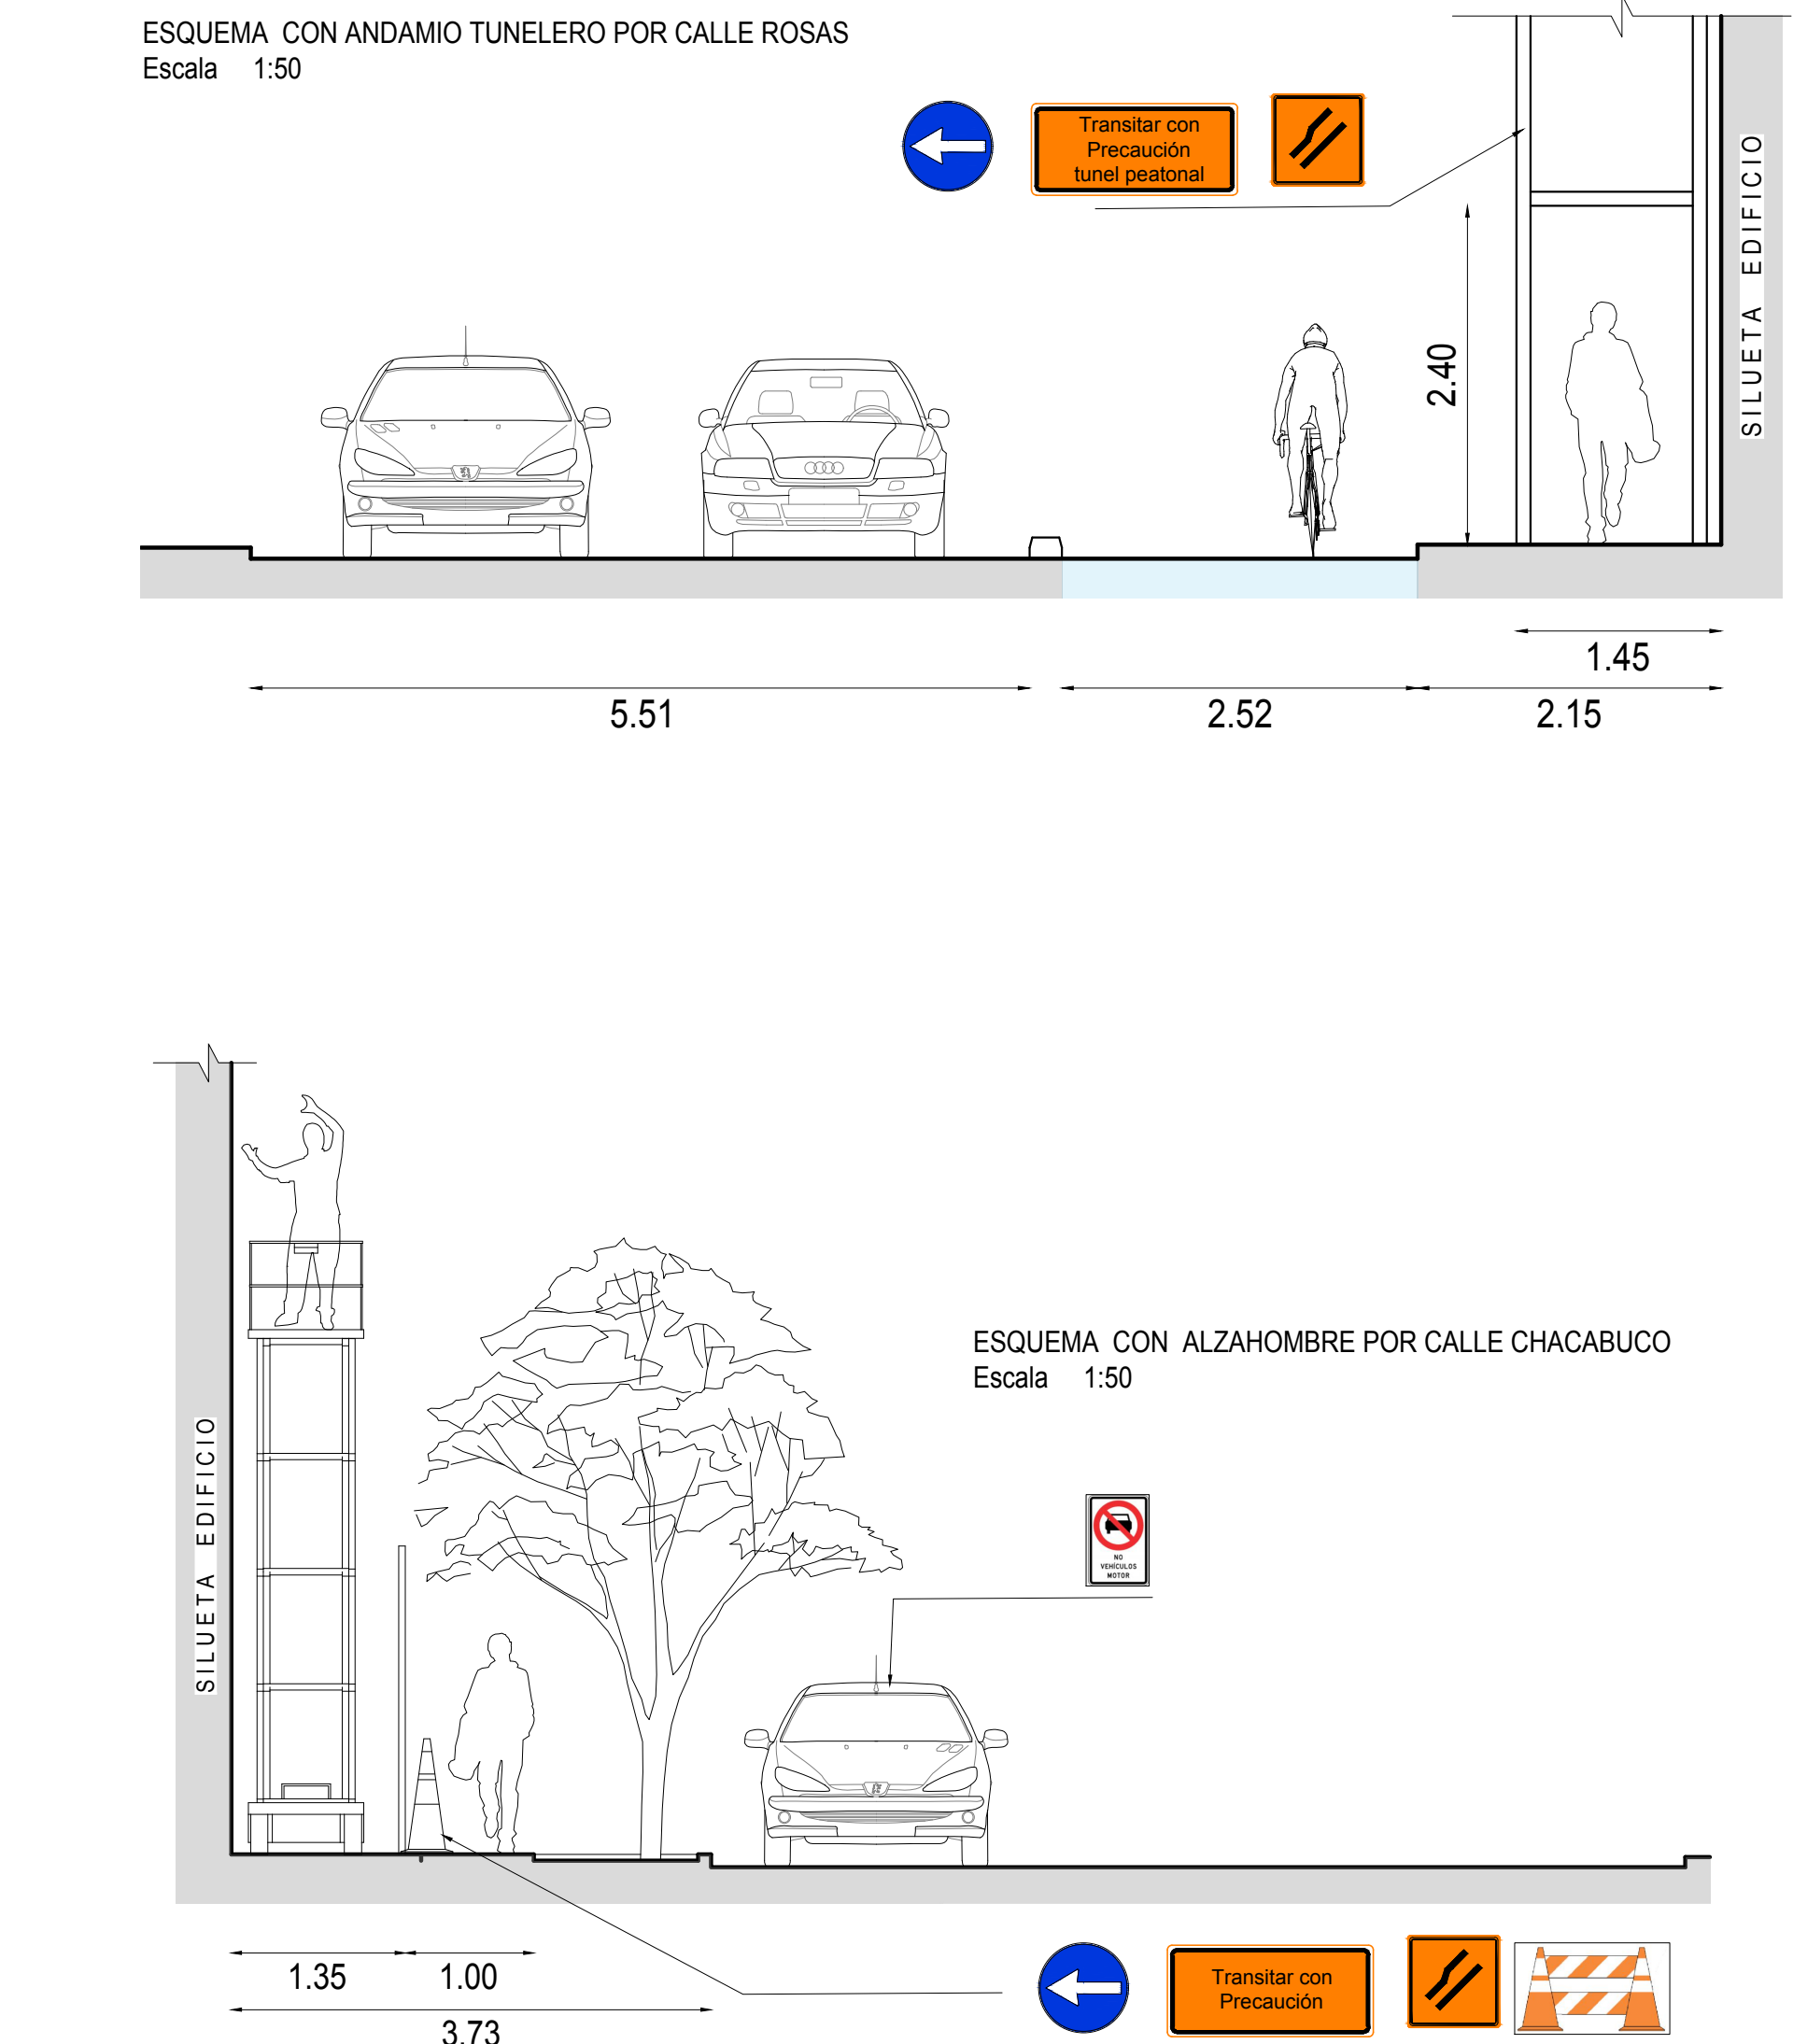


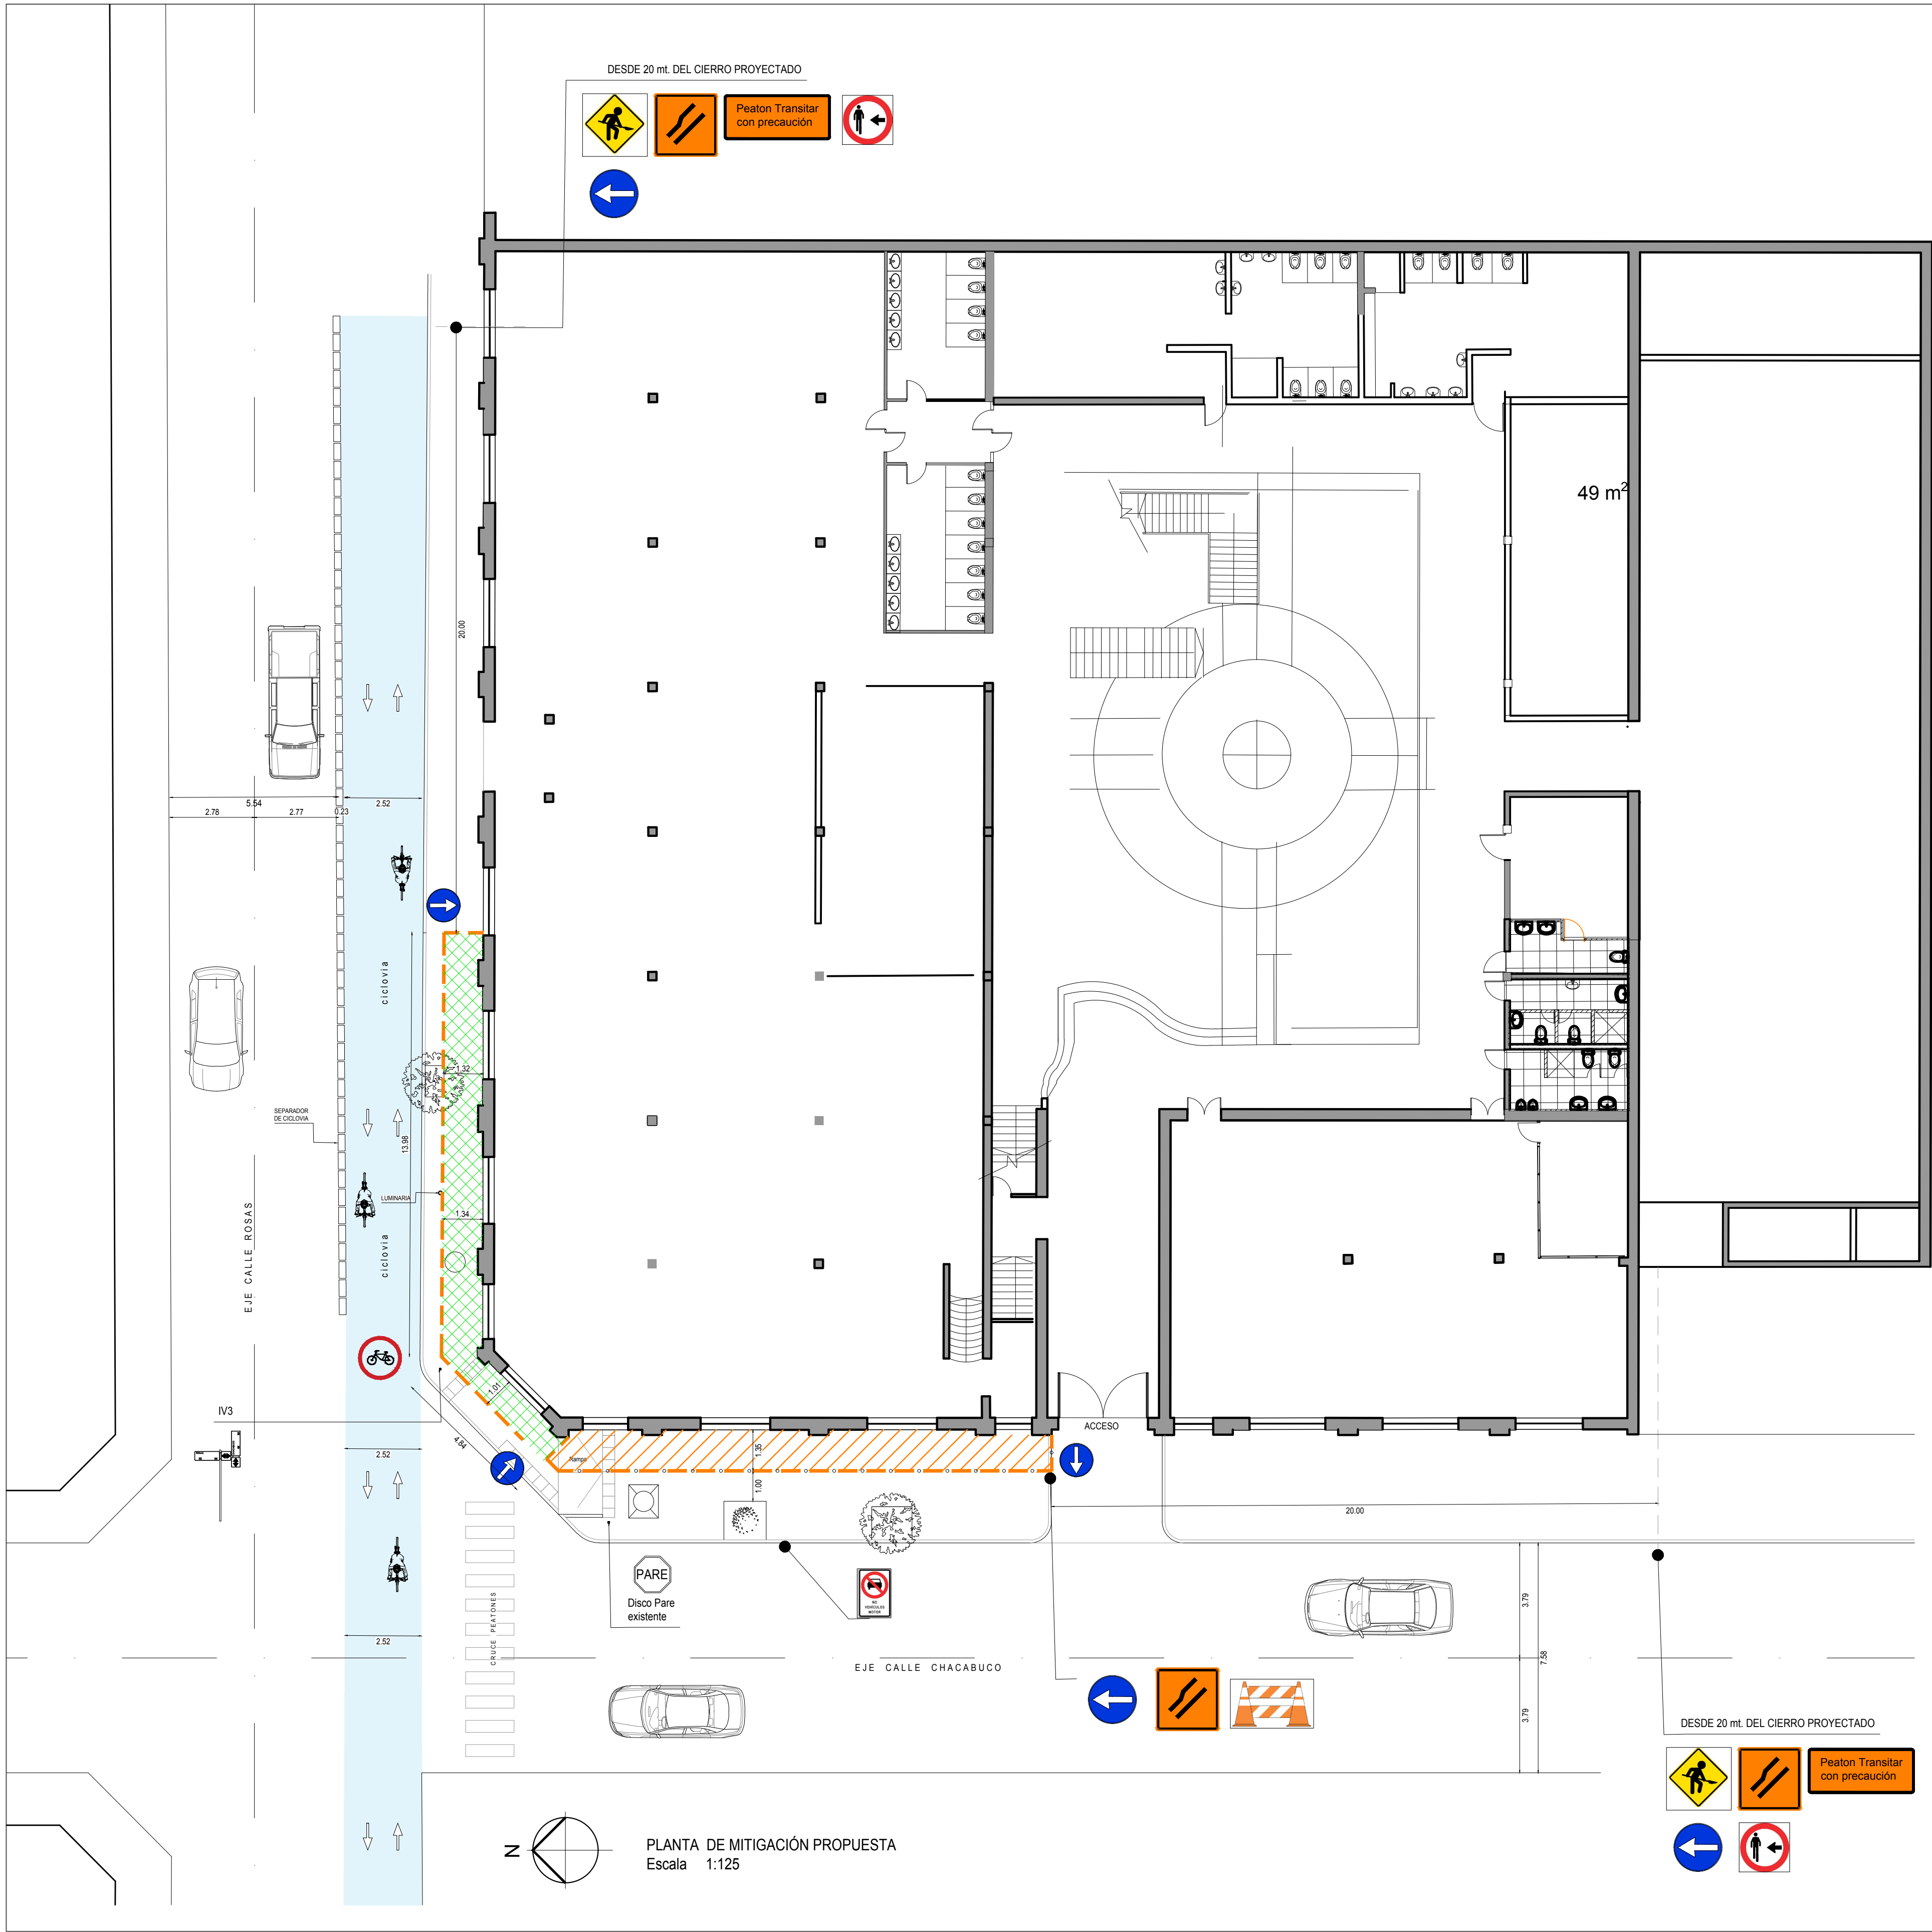

PT - 1		HOMBRES TRABAJANDO
PT - 3		SEÑAL BANDERERO
PTF - 5		ALTURA MÁXIMA
PO - 2		ANGOSTAMIENTO DE VEREDA
I - 1		TUNEL PEATONAL
I P		PEATON TRANSITA POR VEREDA DEL FRENTE
RO - 6a		PASO OBLIGADO DERECHA
		BARRERA PEATONAL
		CONTROL PARE - SIGA
RO - 5L		PEATON TRANSITAR POR LA IZQUIERDA
RPO - 6		NO ESTACIONAR
		ÁREA DE TRABAJO PARA ALZAHOMBRE
		AREA UBICACIÓN ANDAMIO TUNELERO

SEÑALES DE EMERGENCIA

USUARIOS DE EMERGENCIA

- NOTAS:
Se deberá dar cumplimiento a lo indicado en :
- a) NCH 1411/1. Of 78 "Prevención de riesgos - Parte 1: Letreros de seguridad".
 - b) NCH 1411/2. Of 78 Regula señales y símbolos de seguridad.
 - c) NCH 1411/3 Regula el uso de tarjetas de advertencia para riesgos.
 - d) NCH 1411/4 Identificación de Riesgos.
 - e) Decreto N° 78 que aprueba el Manual de Señalización de Tránsito, del Ministerio de Transportes y Telecomunicaciones
 - f) Circular N° 355 que contiene criterios para la elaboración del Plan de Evacuación. Dirección de Desarrollo Urbano, MINVU.
 - g) NCH 3690:2022 Símbolos gráficos - Señales y colores de seguridad - Señales de seguridad con el propósito de la prevención de accidentes, la protección contra incendios, la información sobre peligros para la salud y evacuación de emergencia.
 - h) NCH 1410/1:2012 Símbolos gráficos - Colores de seguridad y señales de seguridad - Parte 1: Principios de diseño para señales de seguridad y marcas de seguridad.
 - i) NCH 1410/3:2021 Símbolos gráficos - Colores de seguridad y señales de seguridad - Parte 3: Principios de diseño para símbolos gráficos para uso de señales de seguridad
 - j) Ley General de Urbanismo y Construcciones.
 - k) Toda normativa legal aplicable en materia laboral, seguridad y prevención de riesgos.